


Assemble

1

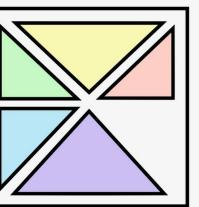

PREFLEX
building

CABIN143SF



PREFLEX OFFICE

No.	Description	Date

Assemble

Project number Project Number


Date Issue Date

Drawn by Author

Checked by Checker


A100

Scale

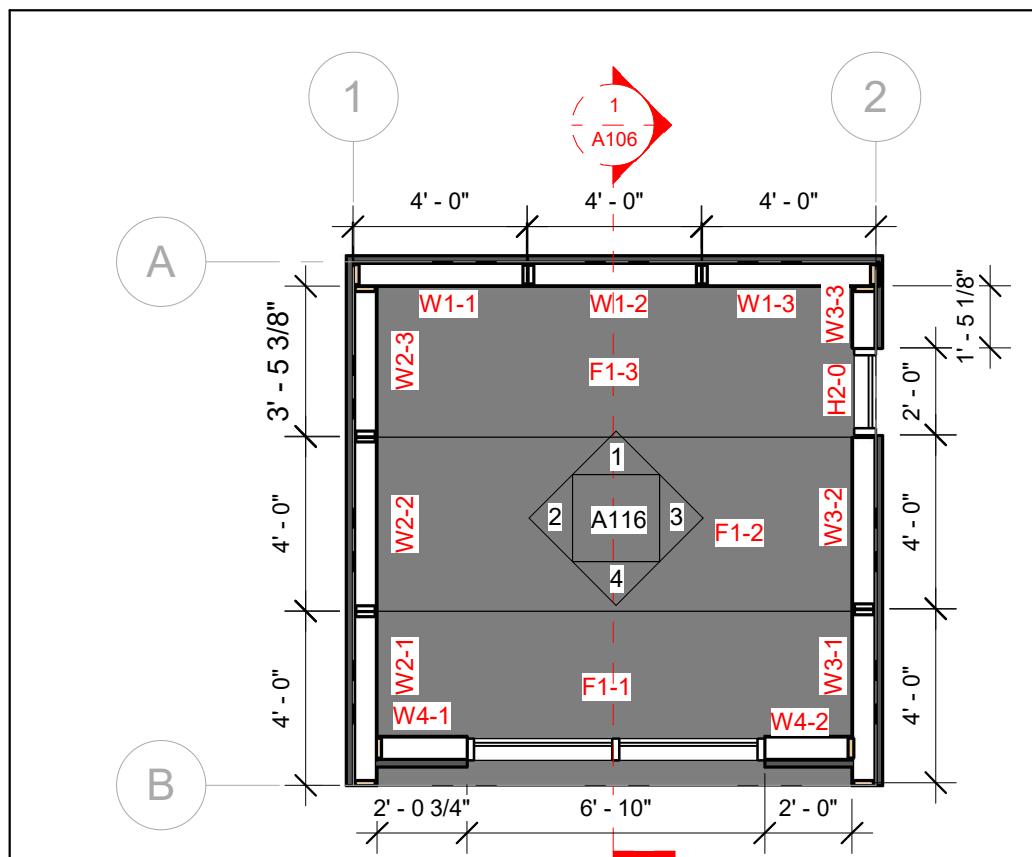


Level 1

1 **LEVEL 1**

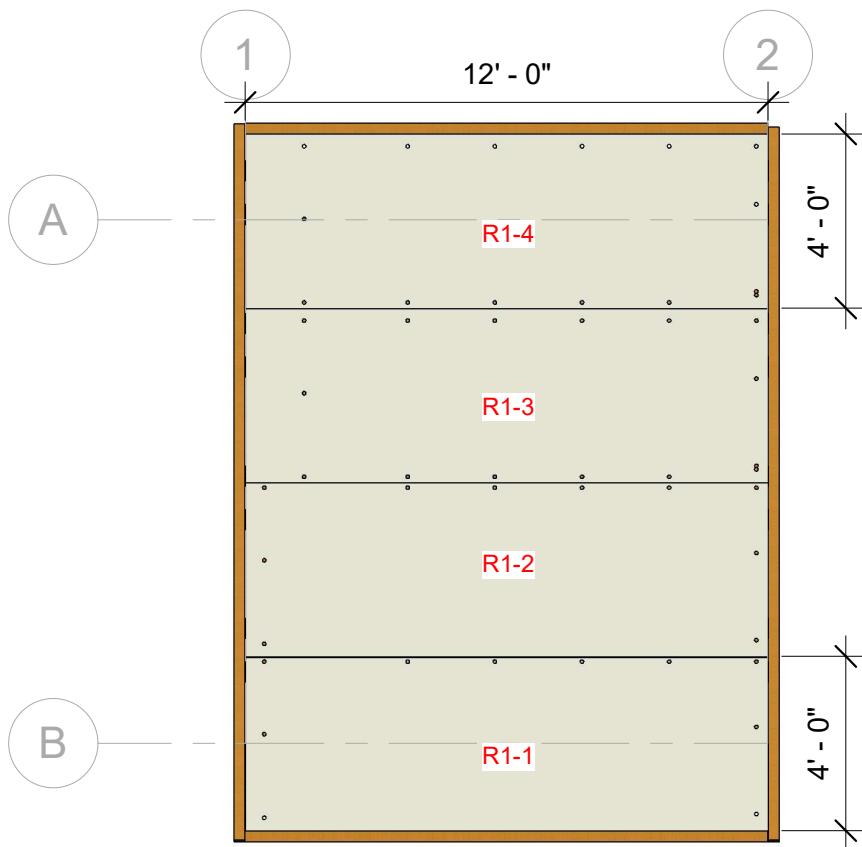

Site

2 $1/4"$ = 1'-0"

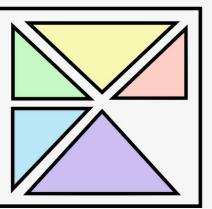

P R E F L E X

b u i l d i n g

CABIN143SF




P R E F L E X O F F I C E


Plan and Roof

Project number	Project Number
Date	Issue Date
Drawn by	Author
Checked by	Checker
A101	
Scale	1/4" = 1'-0"

A101

1/4" = 1'-0"

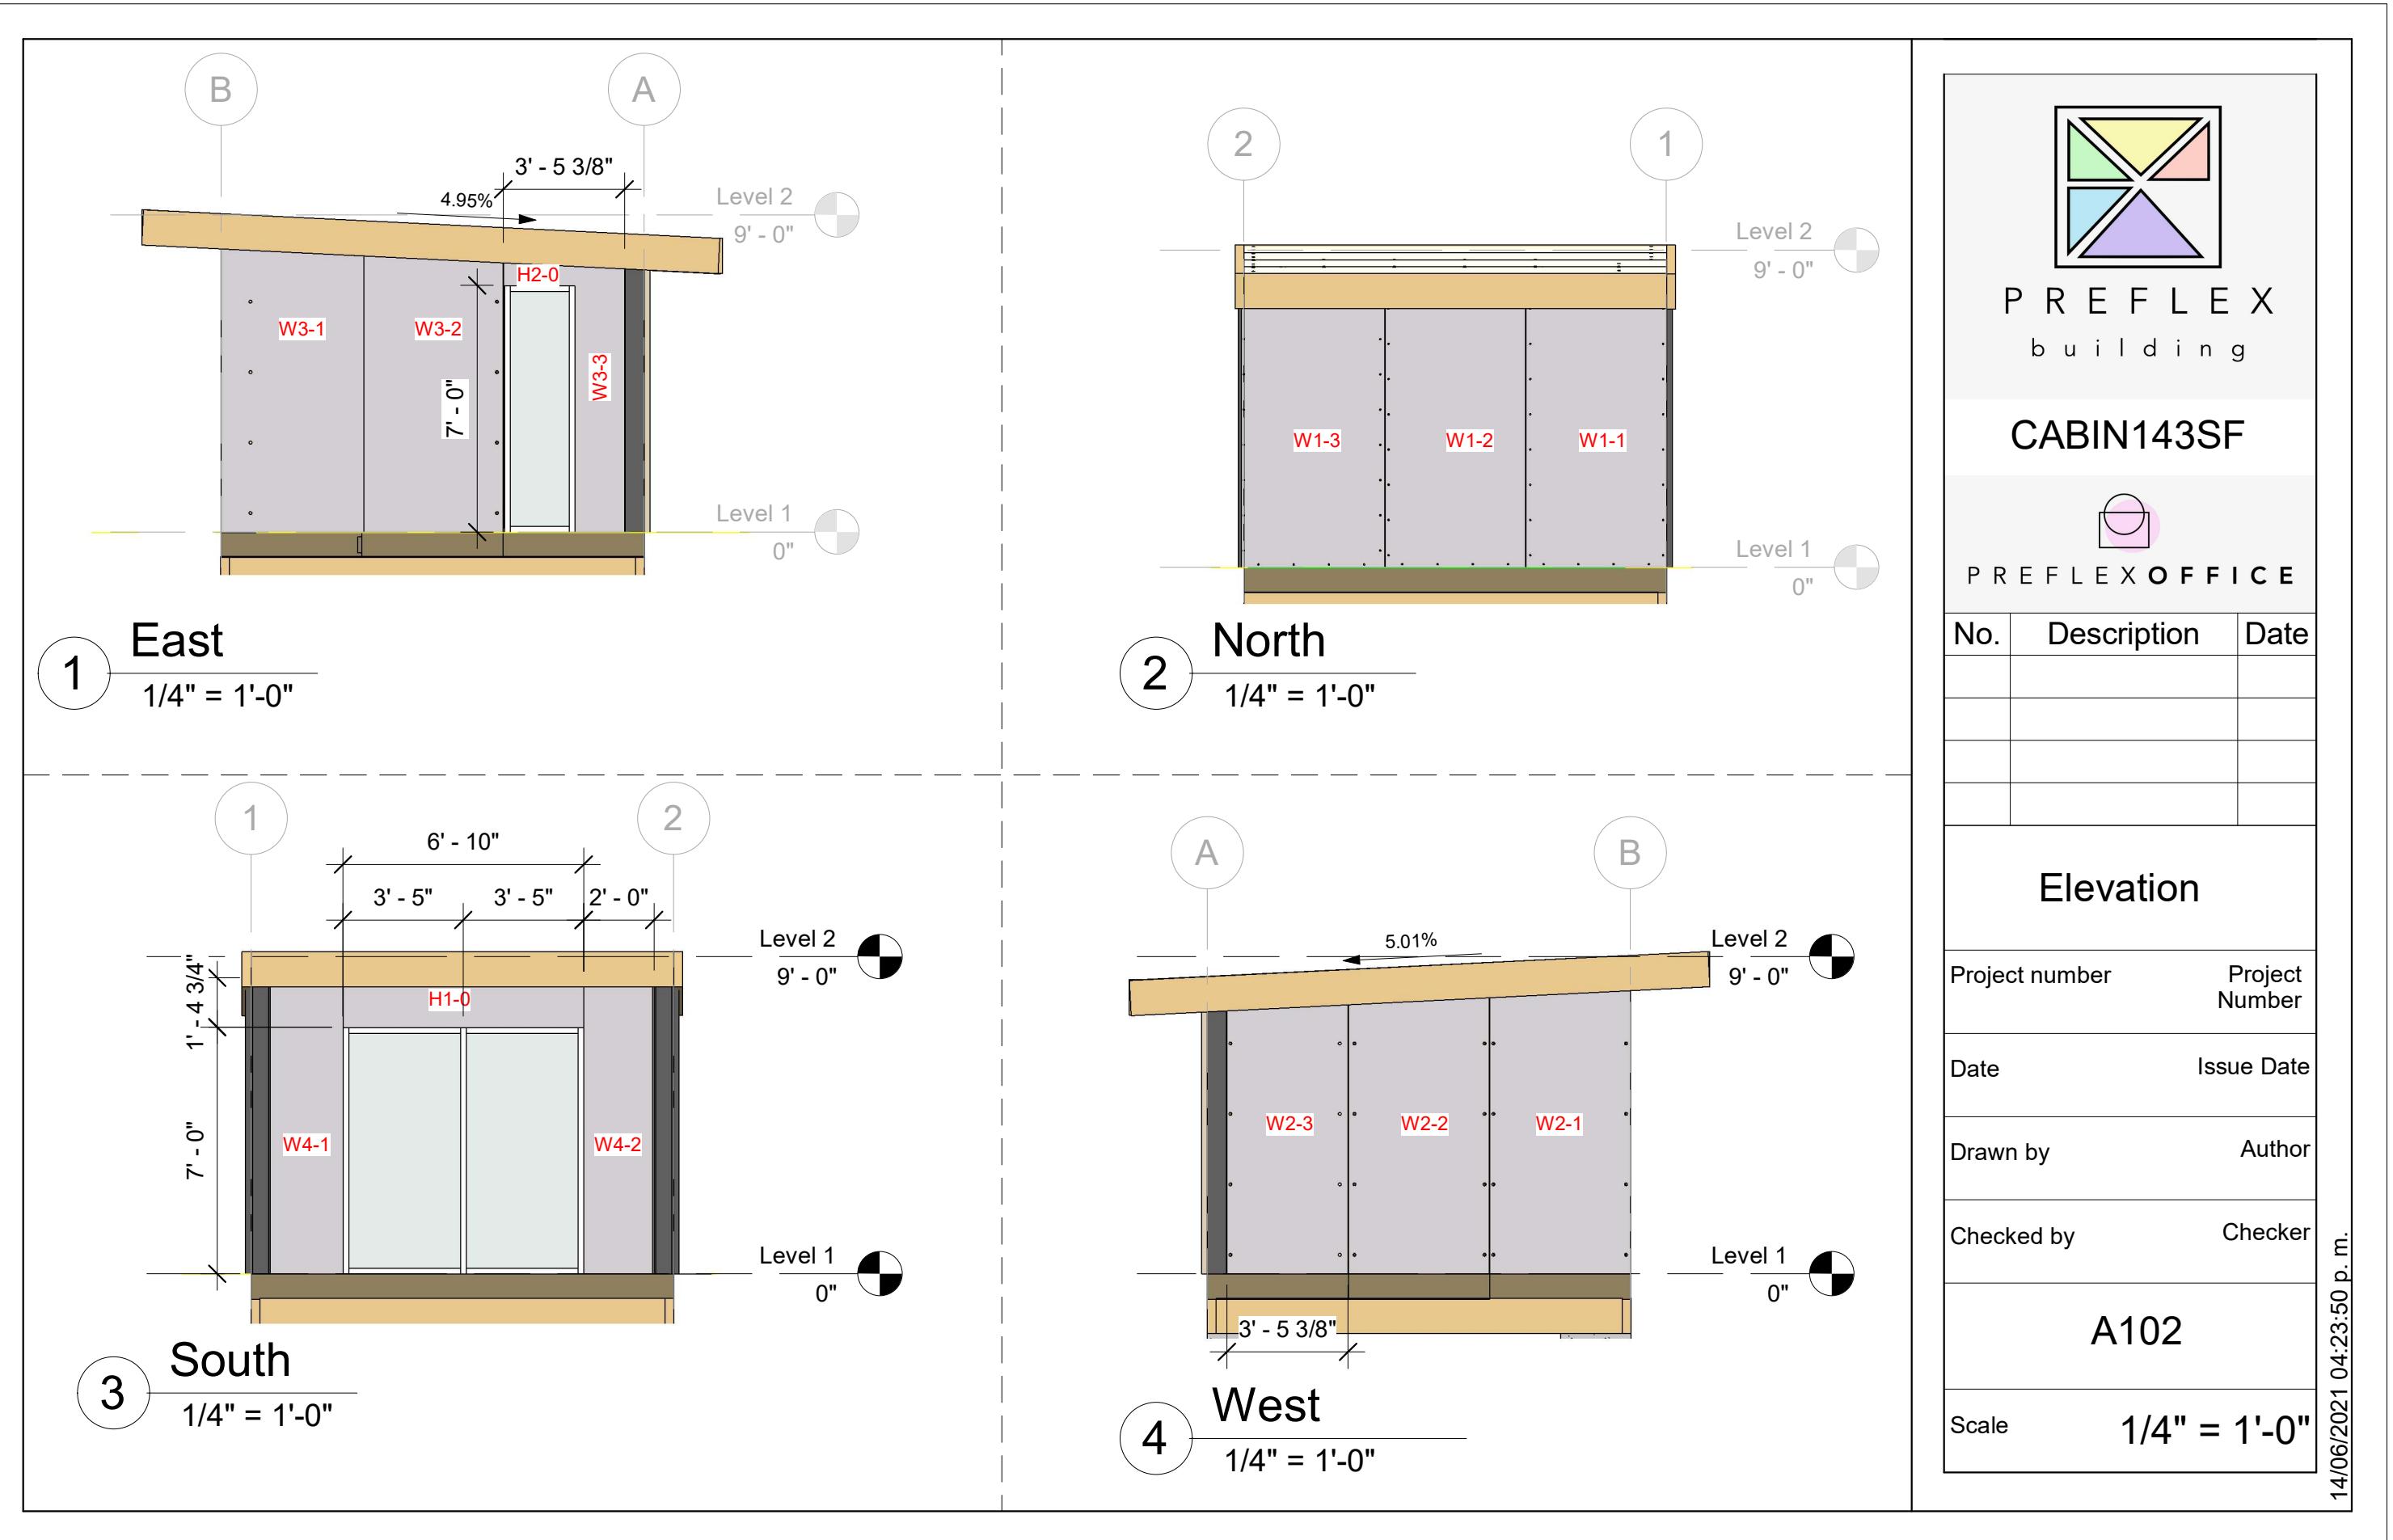

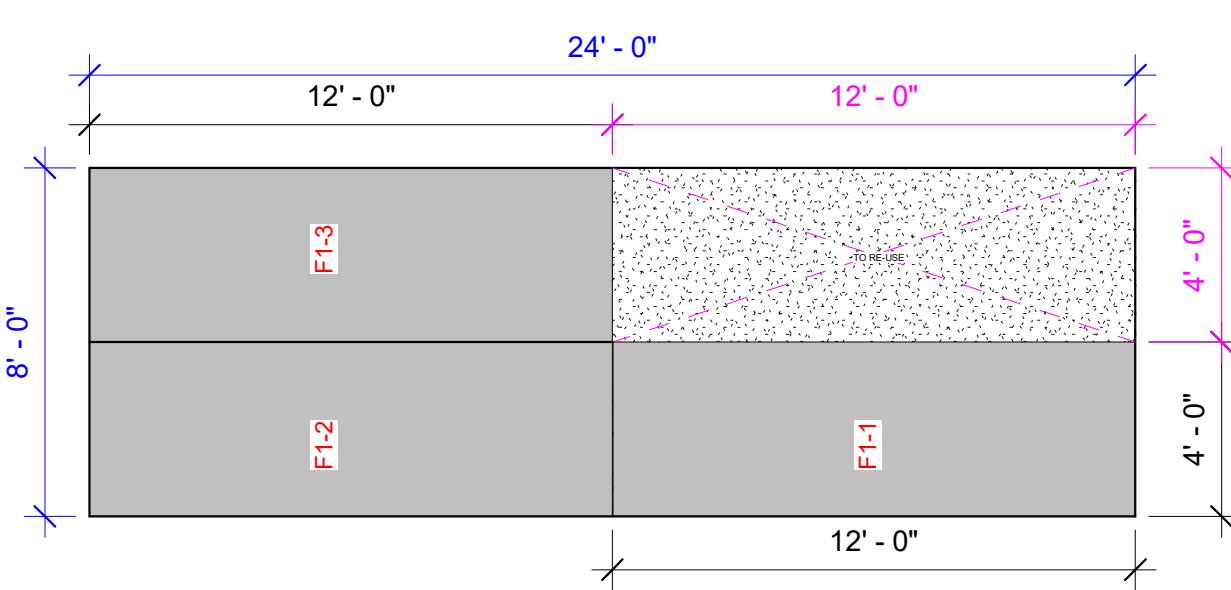

F-PANEL 1

1
1/4" = 1'-0"

Floor Schedule			
Comments	Area	Type	Default Thickness
F1-2	48.13 SF	Floor_SPI_8"	8 1/2"
F1-1	47.96 SF	Floor_SPI_8"	8 1/2"
F1-2	48.00 SF	Floor_SPI_8"	8 1/2"
Grand total: 3	144.08 SF		


F1-2	48.13 SF	Floor_SPI_8"	8 1/2"
F1-1	47.96 SF	Floor_SPI_8"	8 1/2"
F1-2	48.00 SF	Floor_SPI_8"	8 1/2"

TOTAL WEIGHT: 512.49 LB

1 PANEL= 192 SQFT

PANEL TO RE-USE IN OTHER PROJECT: 47.96 SF

SCRAP 0%

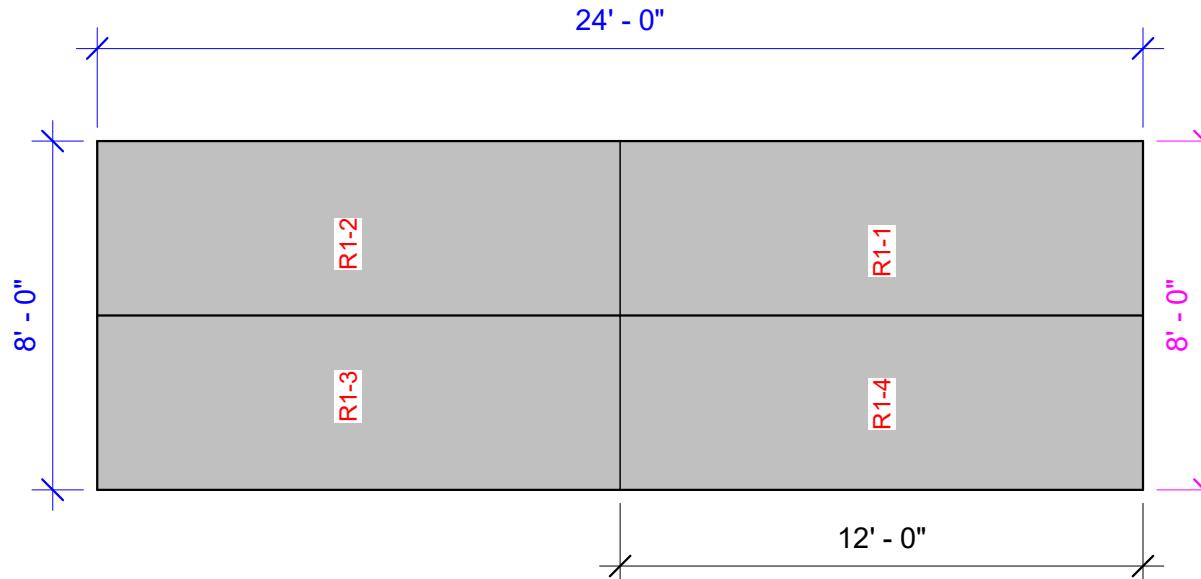

R-PANEL 1

2
1/4" = 1'-0"

Roof Schedule			
Comments	Area	Type	Thickness
R1-1	47.98 SF	Roof_SPI_8"	8 7/8"
R1-1	47.98 SF	Roof_SPI_8"	8 7/8"
R1-1	48.01 SF	Roof_SPI_8"	8 7/8"
R1-1	48.01 SF	Roof_SPI_8"	8 7/8"
Grand total: 4	191.97 SF		


R1-1	47.98 SF	Roof_SPI_8"	8 7/8"
R1-1	47.98 SF	Roof_SPI_8"	8 7/8"
R1-1	48.01 SF	Roof_SPI_8"	8 7/8"
R1-1	48.01 SF	Roof_SPI_8"	8 7/8"
Grand total: 4	191.97 SF		

TOTAL WEIGHT: 683.98 LB

1 PANEL= 192 SQFT

PANEL TO RE-USE IN OTHER PROJECT: 96 SF

SCRAP 3.28%

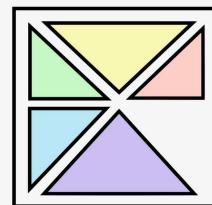

P R E F L E X
b u i l d i n g

CABIN143SF



P R E F L E X O F F I C E

No.	Description	Date

Floor and
Roof_Modulation
for Cutting

Project number	Project Number


Date	Issue Date

Drawn by	Author

Checked by	Checker


A103

Scale	1/4" = 1'-0"

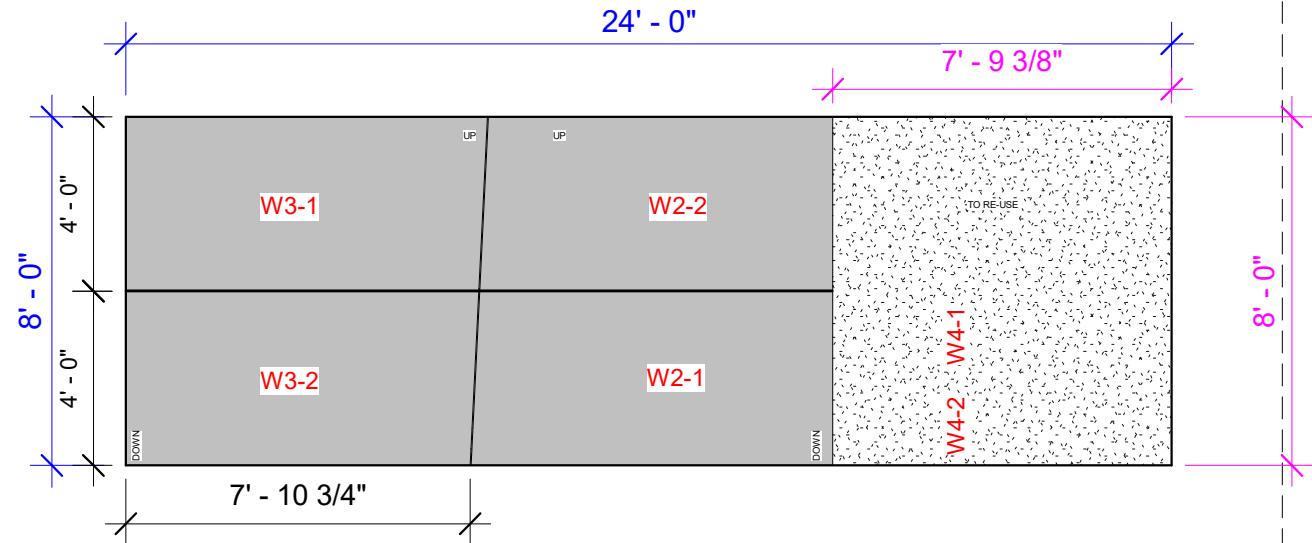

W-PANEL 1

1/4" = 1'-0"

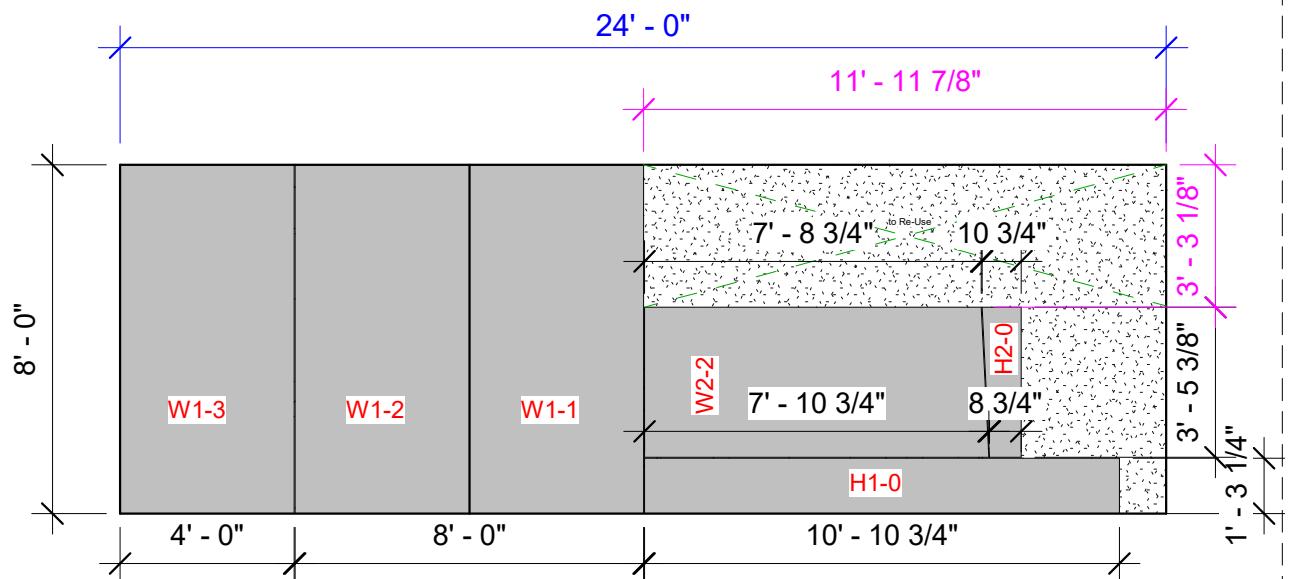

W-PANEL 2

1/4" = 1'-0"

Wall Schedule			
Comments	Area	Type	Width
H2-0	1.68 SF	WALL_SPI_6"	6 5/8"
H1-0	8.69 SF	WALL_SPI_6"	6 5/8"
	11.00 SF	WALL_SPI_6"	6 5/8"
W4-2	16.20 SF	WALL_SPI_6"	6 5/8"
W4-1	17.04 SF	WALL_SPI_6"	6 5/8"
W2-2	26.85 SF	WALL_SPI_6"	6 5/8"
W1-1	30.65 SF	WALL_SPI_6"	6 5/8"
W1-1	30.76 SF	WALL_SPI_6"	6 5/8"
W1-2	31.33 SF	WALL_SPI_6"	6 5/8"
W3-1	31.70 SF	WALL_SPI_6"	6 5/8"
W2-1	31.91 SF	WALL_SPI_6"	6 5/8"
W2-1	32.71 SF	WALL_SPI_6"	6 5/8"
W3-1	33.16 SF	WALL_SPI_6"	6 5/8"


Grand total: 13 303.67 SF

TOTAL WEIGHT: 994.60 LB

2 PANEL= 384 SQFT

PANEL TO RE-USE IN OTHER PROJECT: 70.15 SF

SCRAP 3.95%

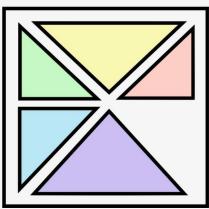

P R E F L E X
b u i l d i n g

CABIN143SF




P R E F L E X O F F I C E

No.	Description	Date

Walls_Modulation for Cutting

Project number	Project Number
Date	Issue Date
Drawn by	Author
Checked by	Checker
A104	
Scale	1/4" = 1'-0"

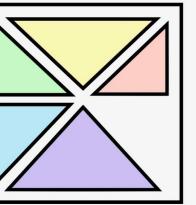

P R E F L E X
b u i l d i n g

CABIN143SF



P R E F L E X O F F I C E

No.	Description	Date

Details

Project number Project Number

Date Issue Date


Drawn by Author



Checked by Checker

A105

Scale As indicated

14/06/2021 04:23:52 p. m.

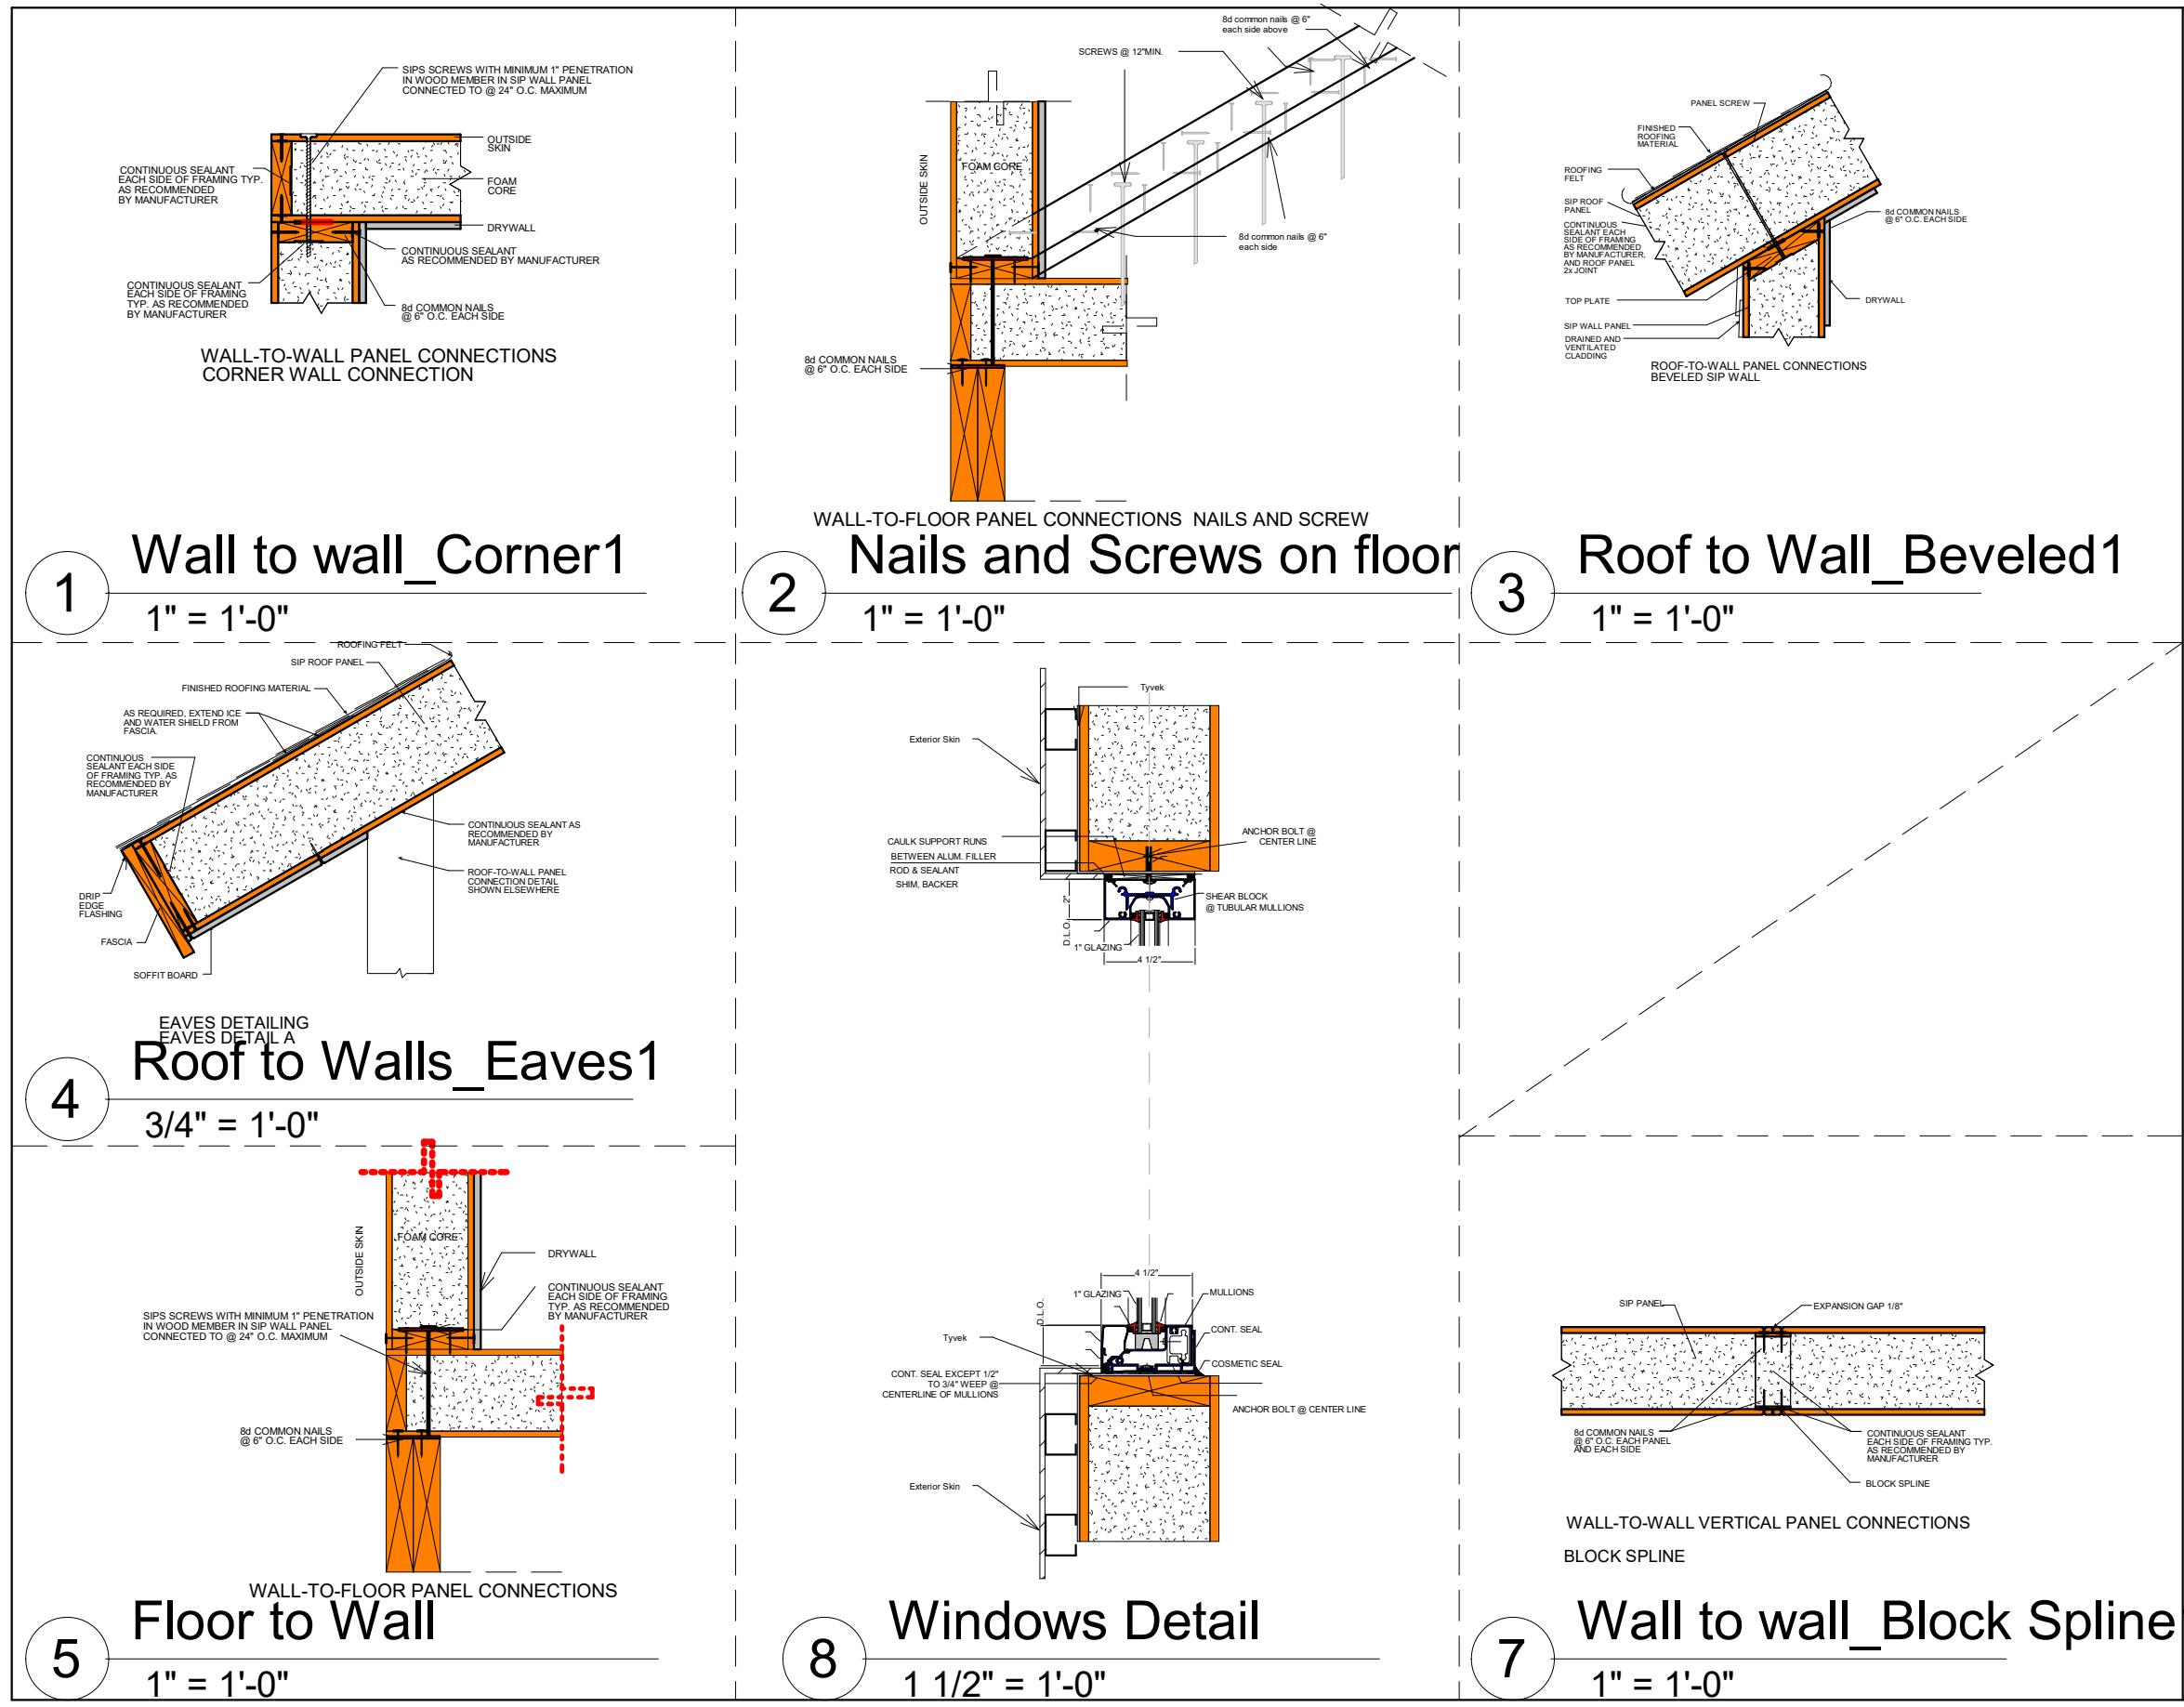

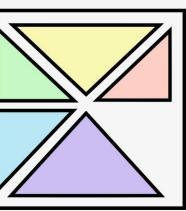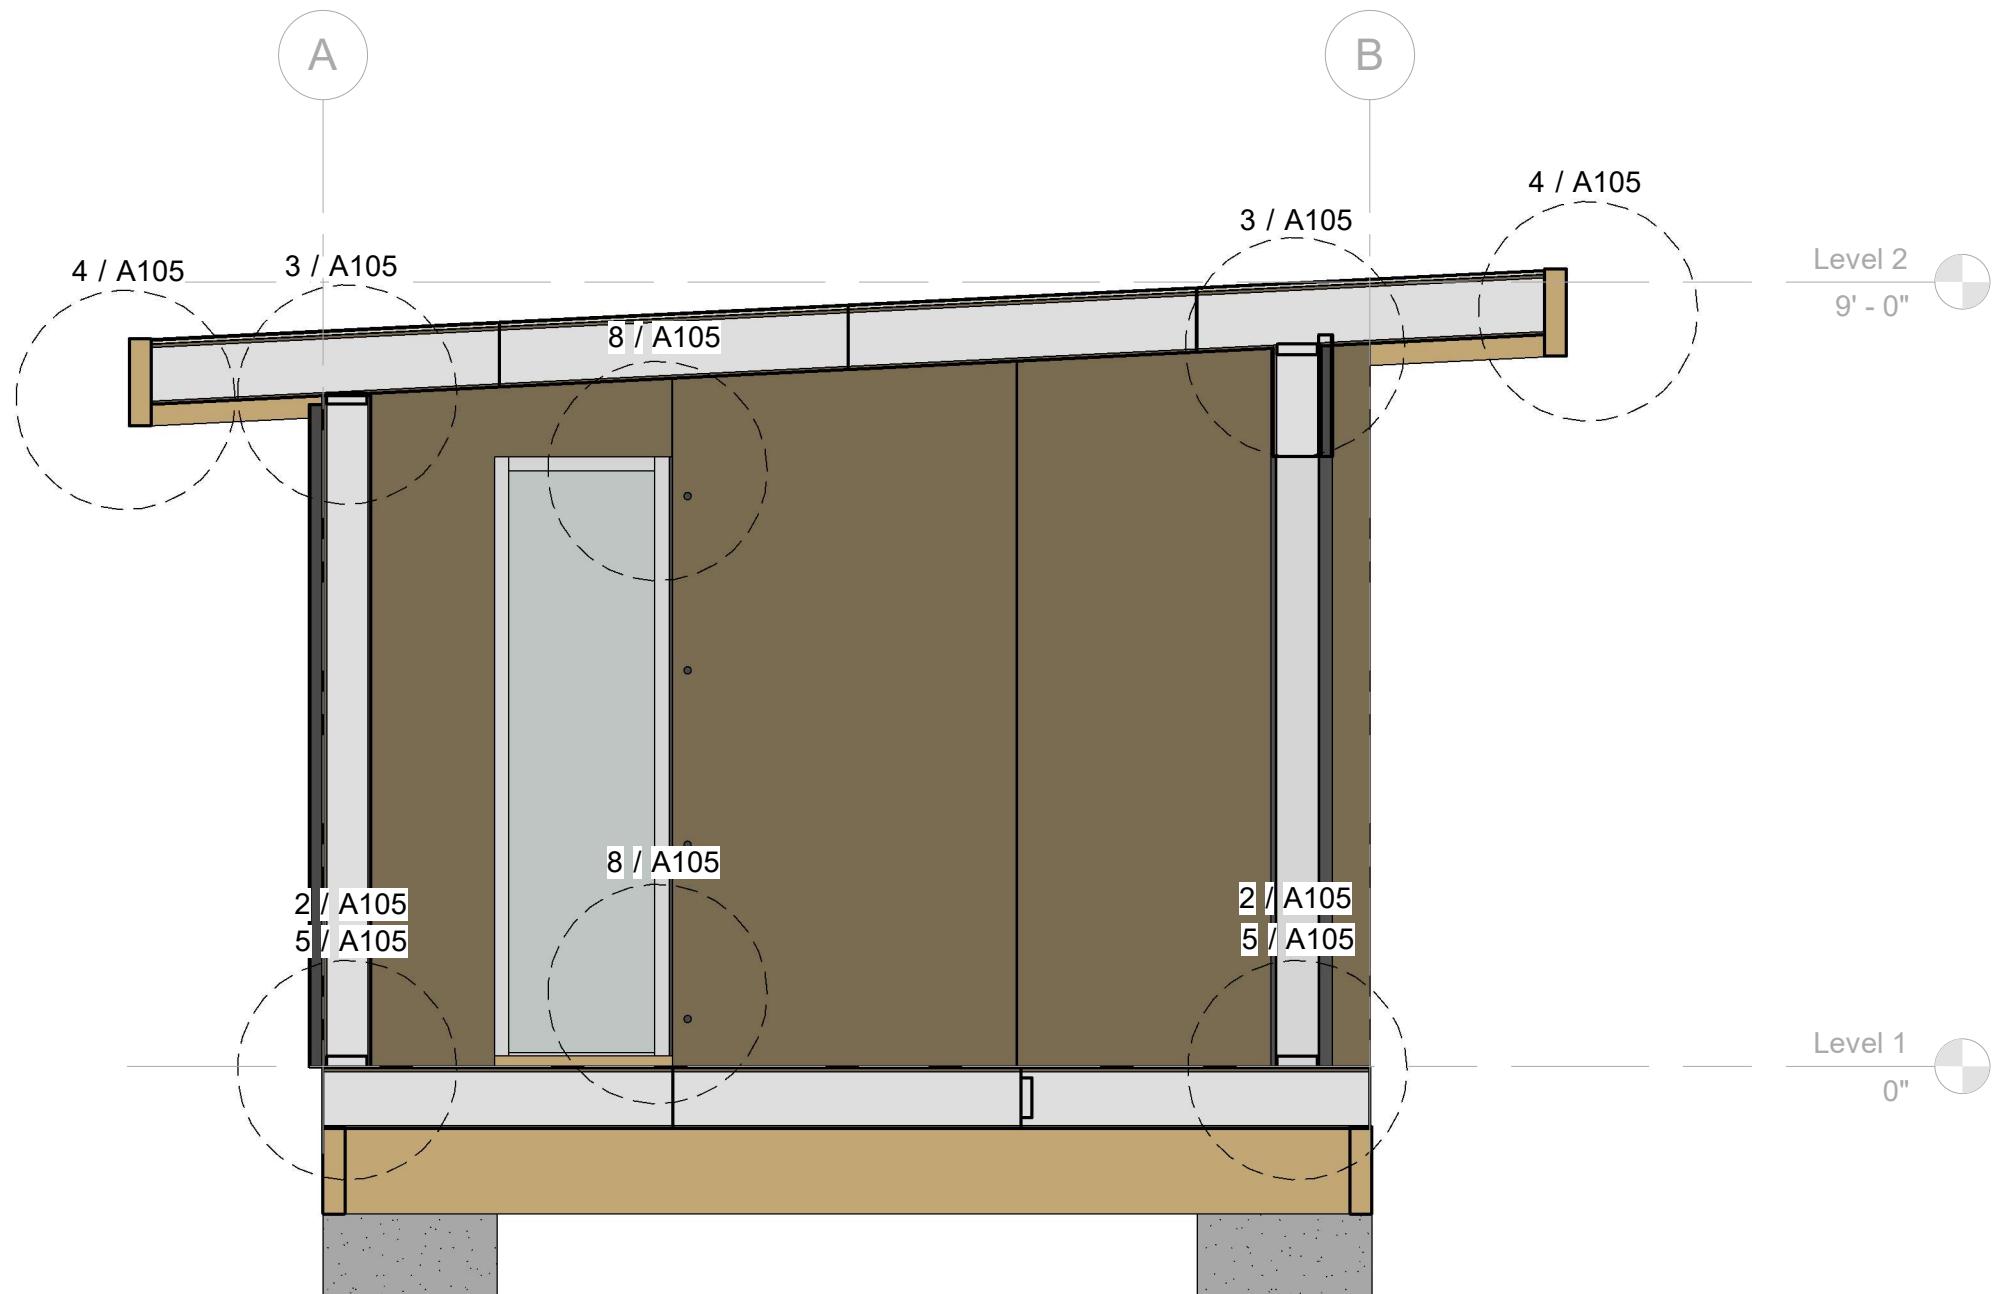

P R E F L E X
b u i l d i n g

CABIN143SF



P R E F L E X O F F I C E

No.	Description	Date

Section

Project number Project Number


Date Issue Date

Drawn by Author

Checked by Checker

A106


Scale 1/2" = 1'-0"

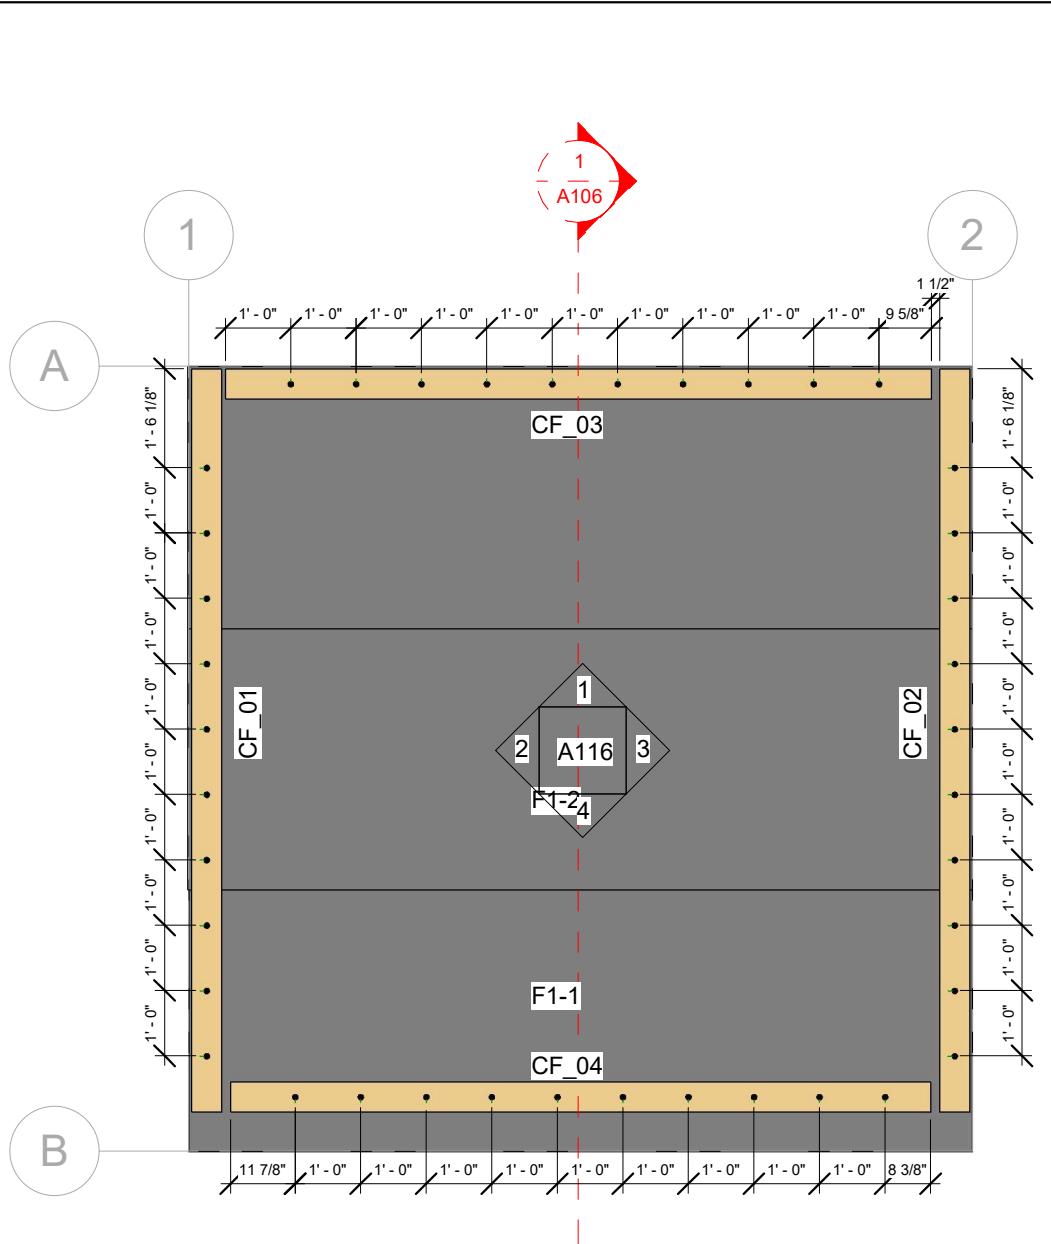


1 Connector to floor
3/8" = 1'-0"

VIEWS DETAILS THAT APPLY:

2 / A105
5 / A105

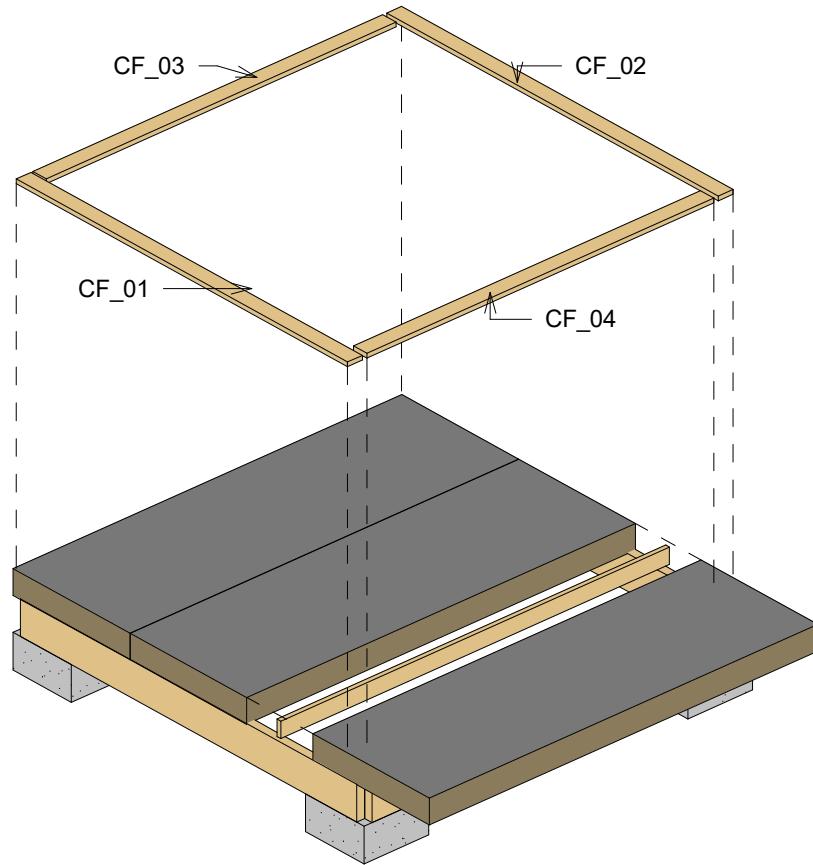

2 Connectors To Floor

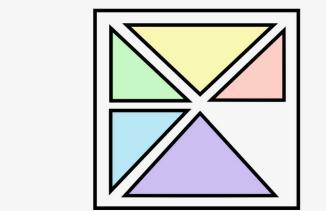

P R E F L E X
b u i l d i n g

CABIN143SF



P R E F L E X O F F I C E

No.	Description	Date

Connectors to Floor

Project number Project Number





Date Issue Date

Drawn by Author

Checked by Checker

A107

Scale 3/8" = 1'-0"

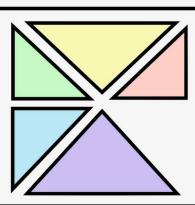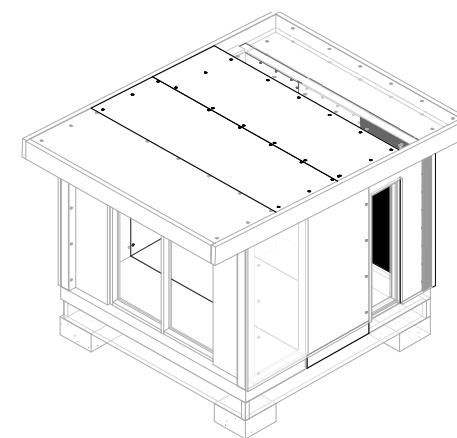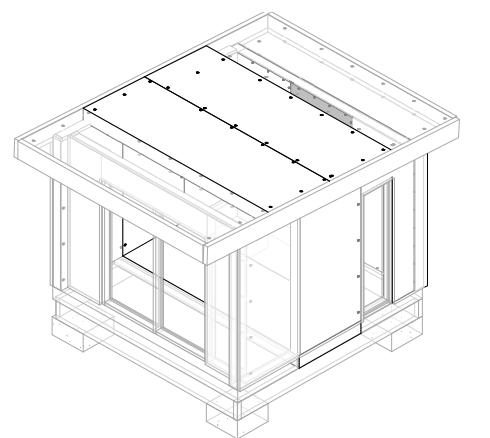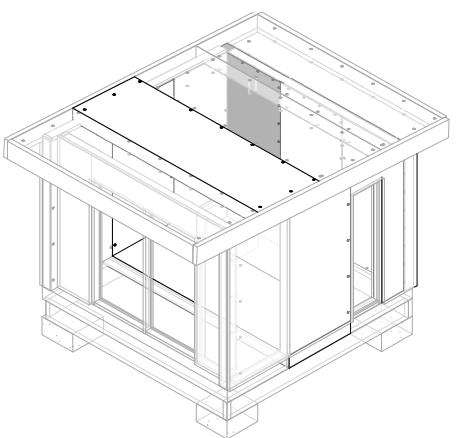

P R E F L E X
b u i l d i n g

CABIN143SF




P R E F L E X O F F I C E

No.	Description	Date

Shop Drawings W1-1, W1-2, W1-3


Project number	Project Number
Date	Issue Date
Drawn by	Author
Checked by	Checker

A108	
Scale	3/8" = 1'-0"

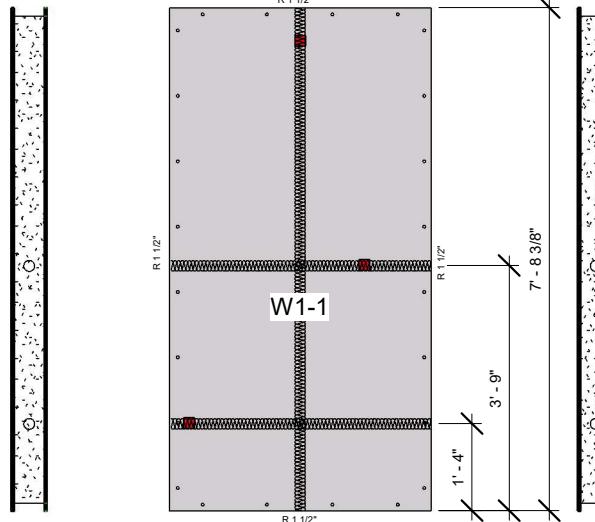


AREA: 30.76 SF
WEIGHT: 102.43 LBS

1 W1-1
3/8" = 1'-0"

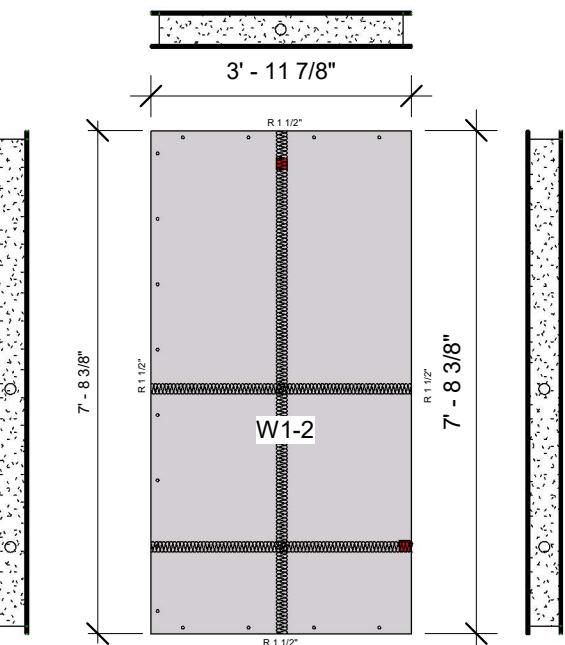







AREA: 30.65 SF
WEIGHT: 102.06 LBS

5 W1-2
3/8" = 1'-0"

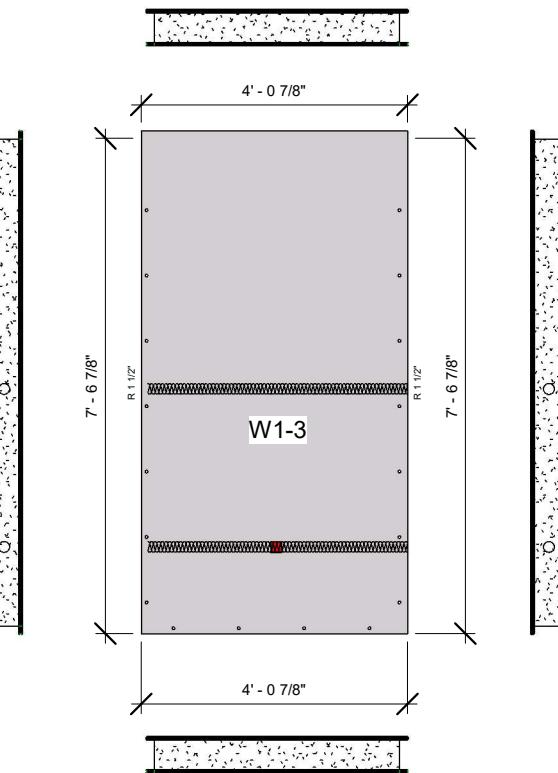

AREA: 31.33 SF
WEIGHT: 104.32 LBS


2 W1-3
3/8" = 1'-0"

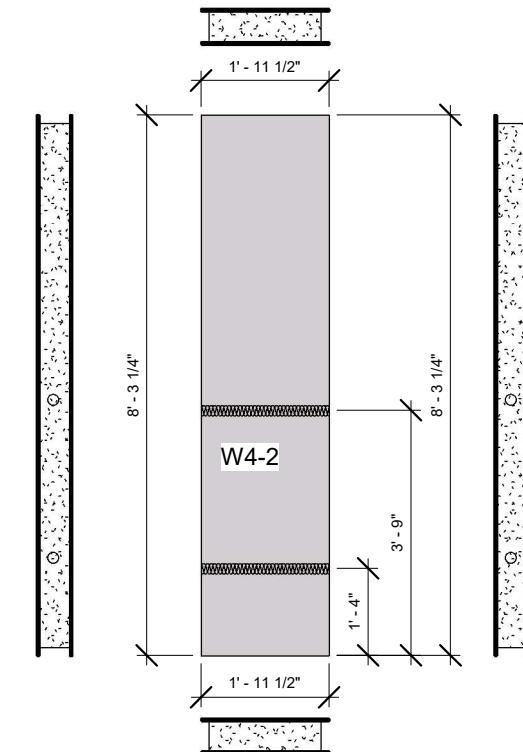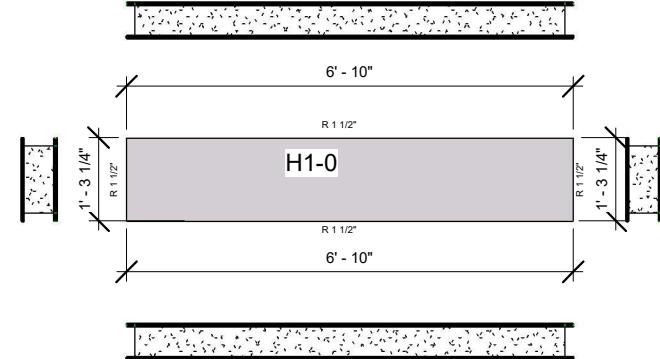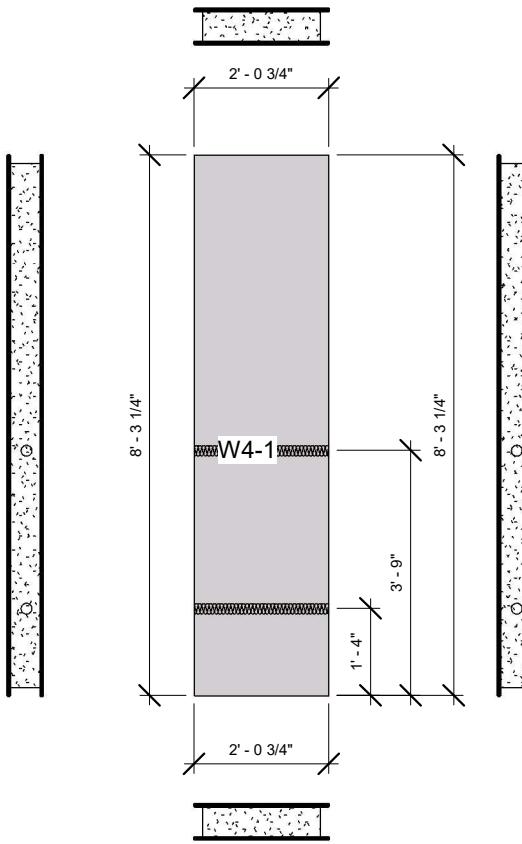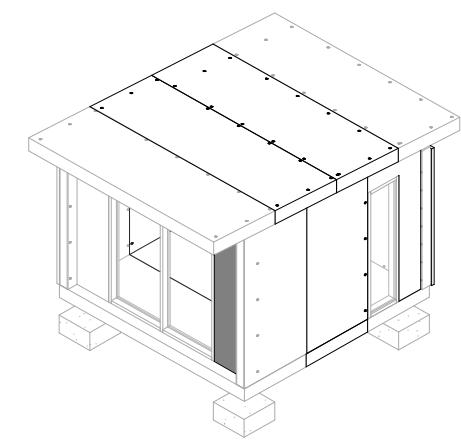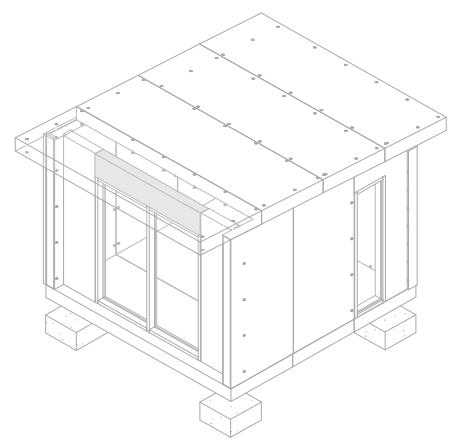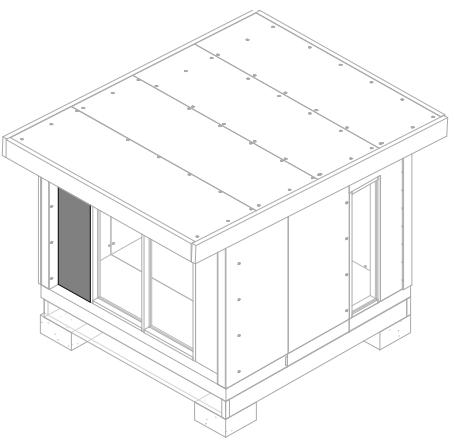

1 W4-1
3/8" = 1'-0"

2 H1-0
3/8" = 1'-0"

3 W4-2
3/8" = 1'-0"

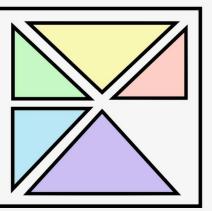

P R E F L E X
b u i l d i n g

CABIN143SF



P R E F L E X O F F I C E

No.	Description	Date
-----	-------------	------

Shop Drawings W4-1, H1-0, W4-2

Project number	Project Number
----------------	----------------









Date	Issue Date
------	------------

Drawn by	Author
----------	--------

Checked by	Checker
------------	---------

A109

Scale	3/8" = 1'-0"
-------	--------------

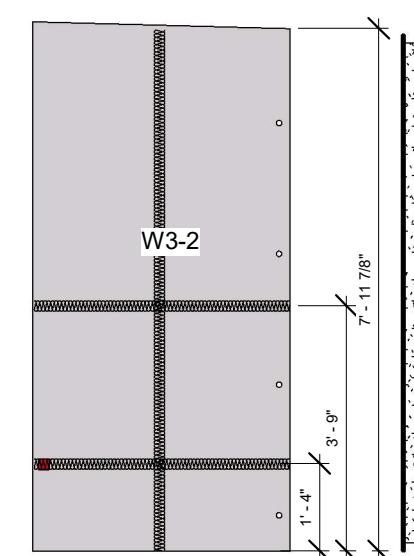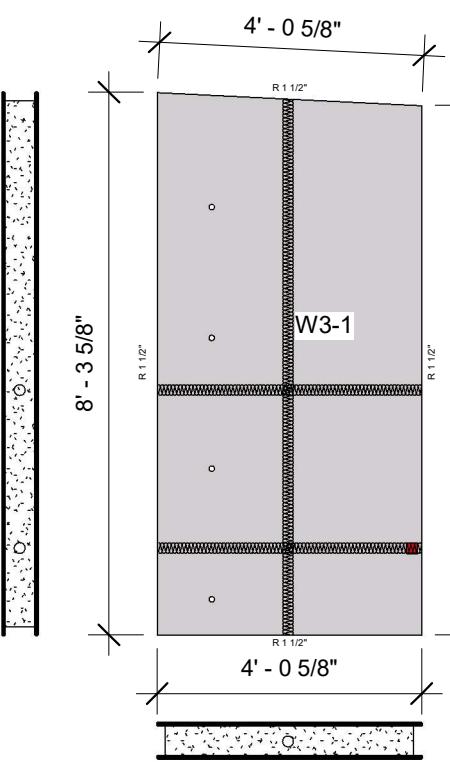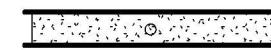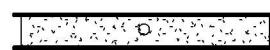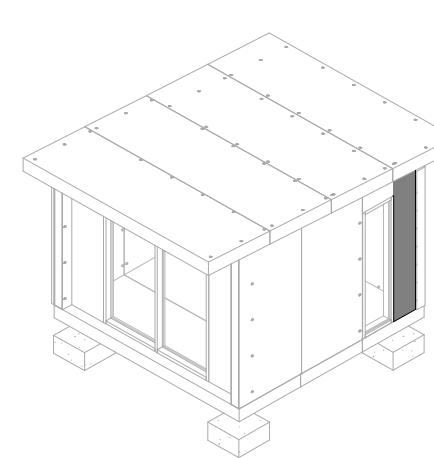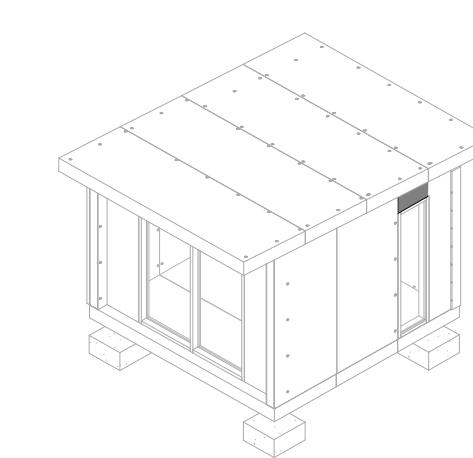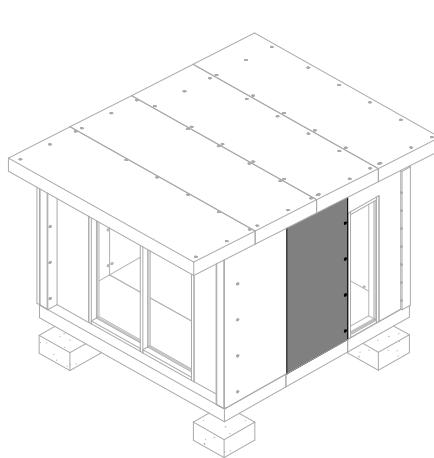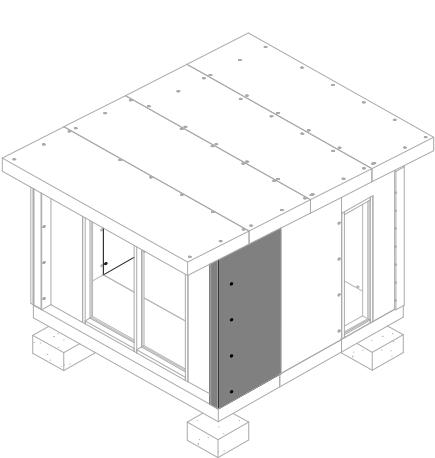

AREA: 2.80 SF
WEIGHT: 9.32 LBS

2 H2-0
3/8" = 1'-0"

2

H2-0
3/8" = 1'-0"

1


W3-1
3/8" = 1'-0"

5

W3-2
3/8" = 1'-0"

2

H2-0
3/8" = 1'-0"

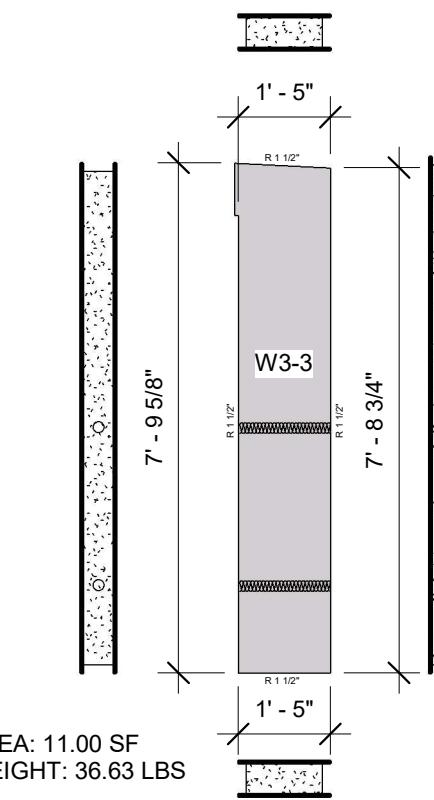


AREA: 11.00 SF
WEIGHT: 36.63 LBS

6 W3-3
3/8" = 1'-0"

6

W3-3
3/8" = 1'-0"

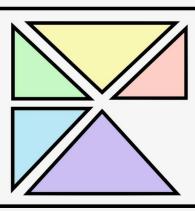

P R E F L E X
b u i l d i n g

CABIN143SF



P R E F L E X O F F I C E





No.	Description	Date

Shop Drawings W3-1, H2-0

Project number	Project Number
Date	Issue Date
Drawn by	Author
Checked by	Checker

A110

Scale 3/8" = 1'-0"

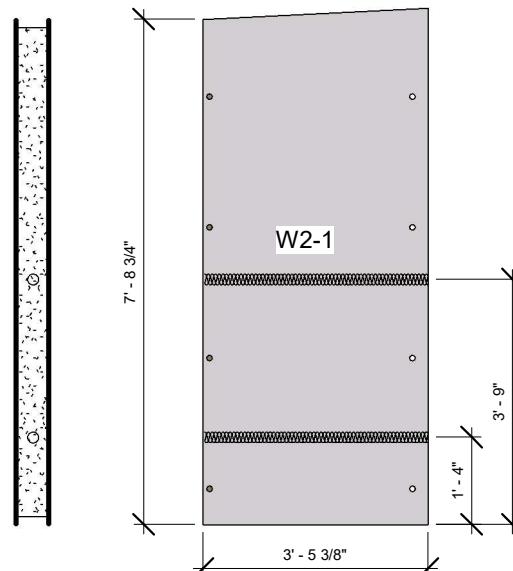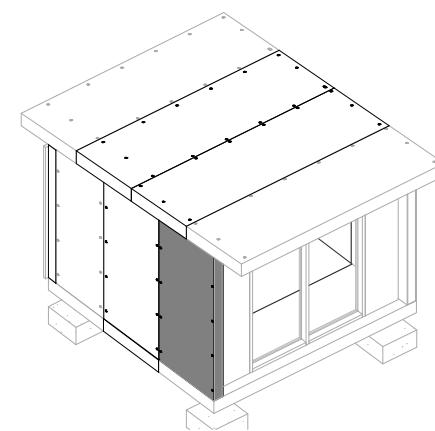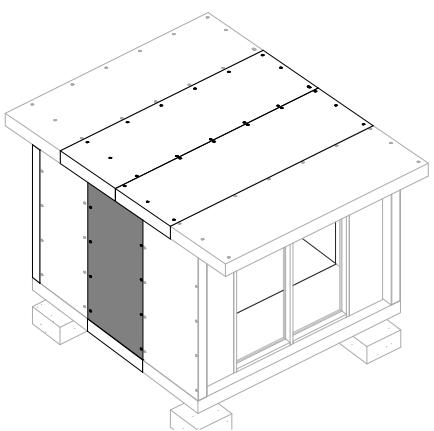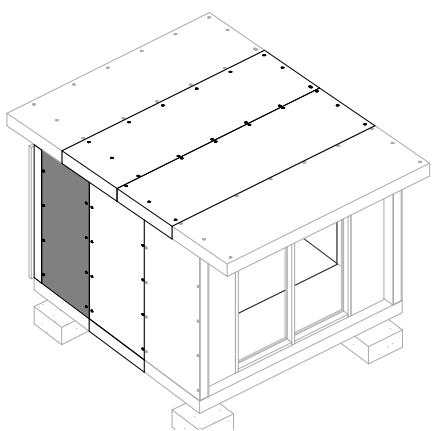

AREA: 26.85 SF
WEIGHT: 89.41 LBS


2 W2-1
3/8" = 1'-0"

AREA: 31.91 SF
WEIGHT: 106.26 LBS

5 W2-2
3/8" = 1'-0"

AREA: 32.71 SF
WEIGHT: 108.92 LBS

1 W2-3
3/8" = 1'-0"

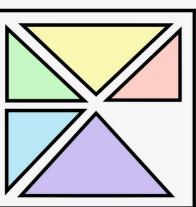

P R E F L E X
b u i l d i n g

CABIN143SF



P R E F L E X O F F I C E

No.	Description	Date

Shop Drawings W2-1, W2-2

Project number Project Number




Date Issue Date

Drawn by Author

Checked by Checker

A111

Scale 3/8" = 1'-0"

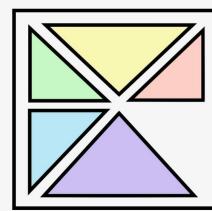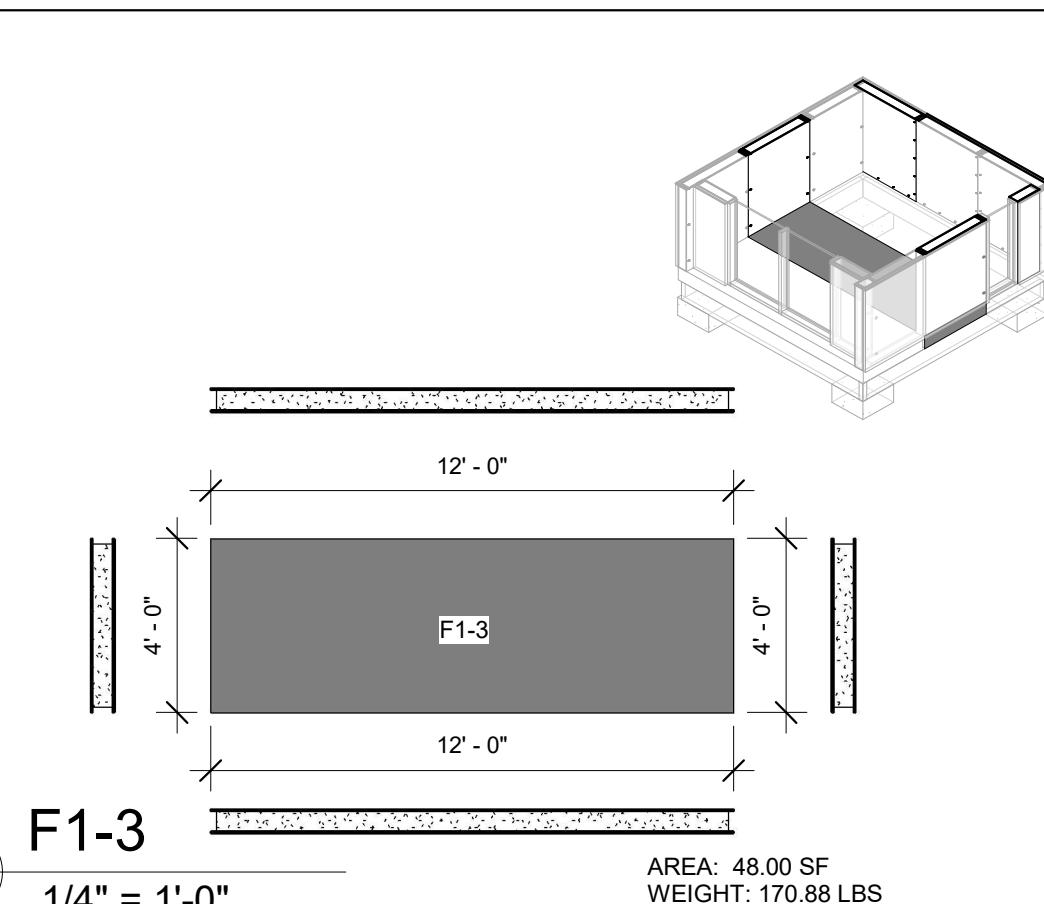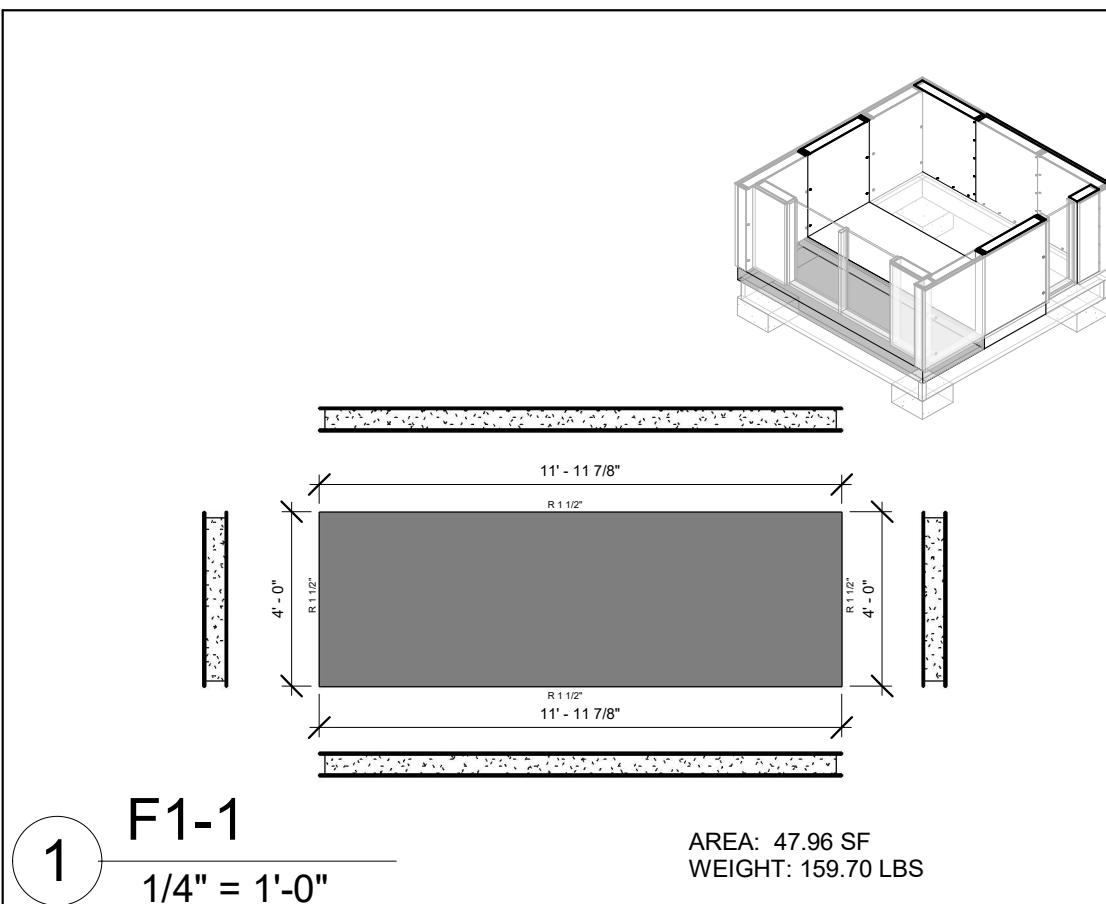

P R E F L E X

b u i l d i n g

CABIN143SF



P R E F L E X O F F I C E


No.	Description	Date

Shop Drawings

F1-1, F1-2, F1-3

Project number	Project Number
Date	Issue Date
Drawn by	Author
Checked by	Checker
A112	
Scale	1/4" = 1'-0"

14/06/2021 04:24:01 p. m.

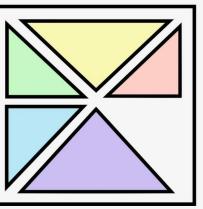

P R E F L E X

b u i l d i n g

CABIN143SF



P R E F L E X O F F I C E





No.	Description	Date

Shop Drawings

R1-1, R1-2, R1-3, R1-4


Project number	Project Number
Date	Issue Date
Drawn by	Author
Checked by	Checker
A113	
Scale	1/4" = 1'-0"

14/06/2021 04:24:02 p. m.

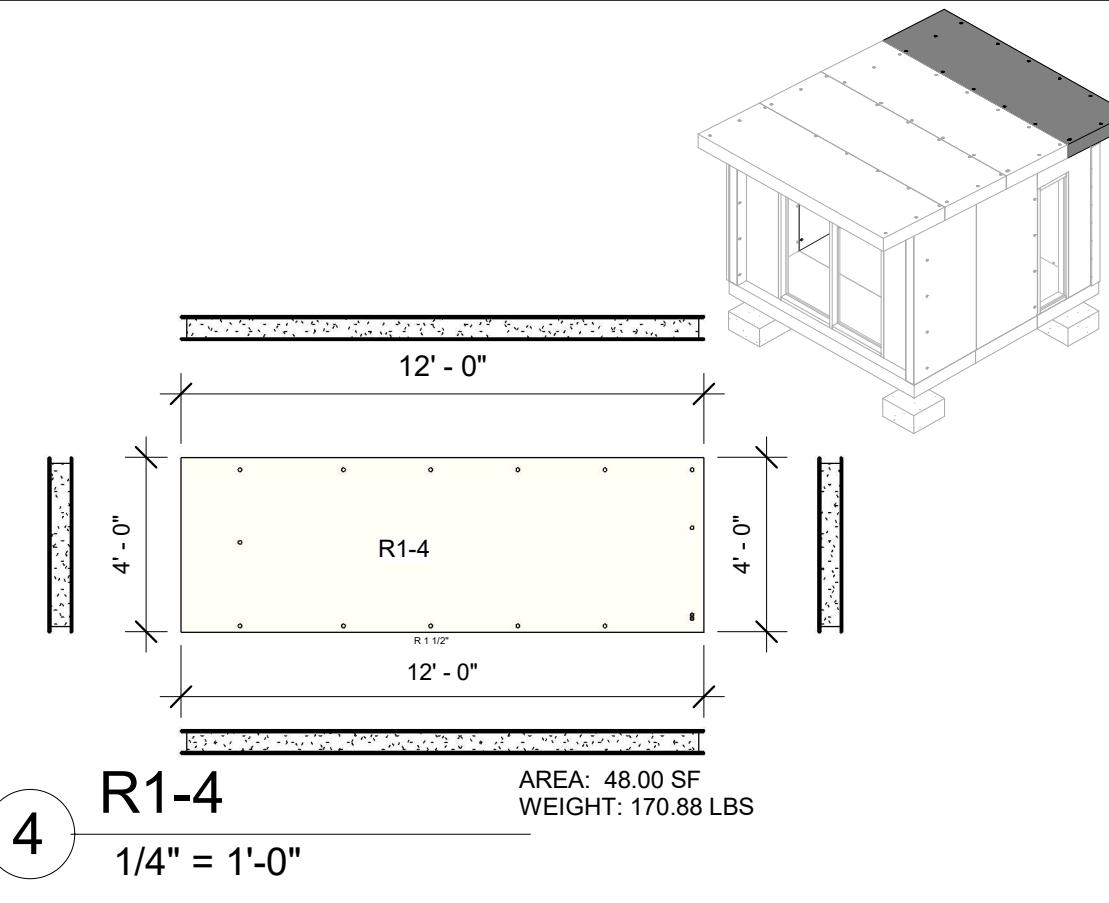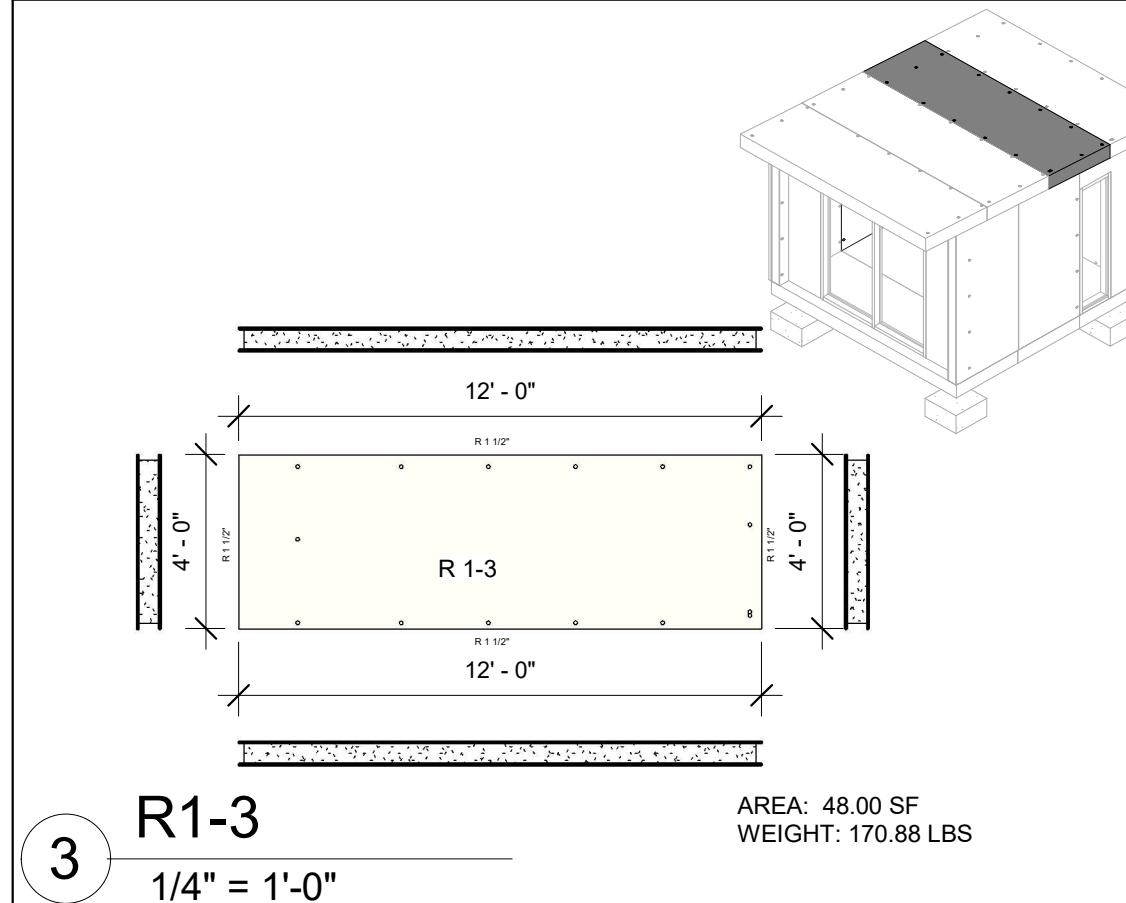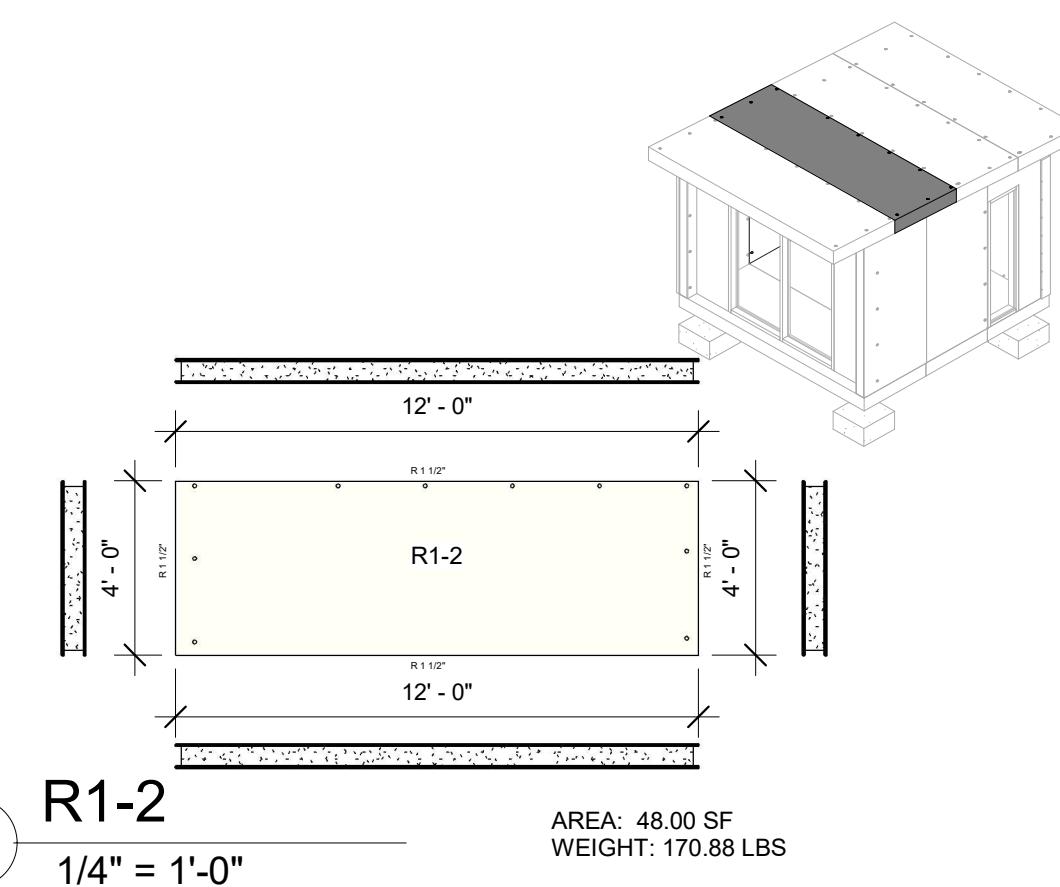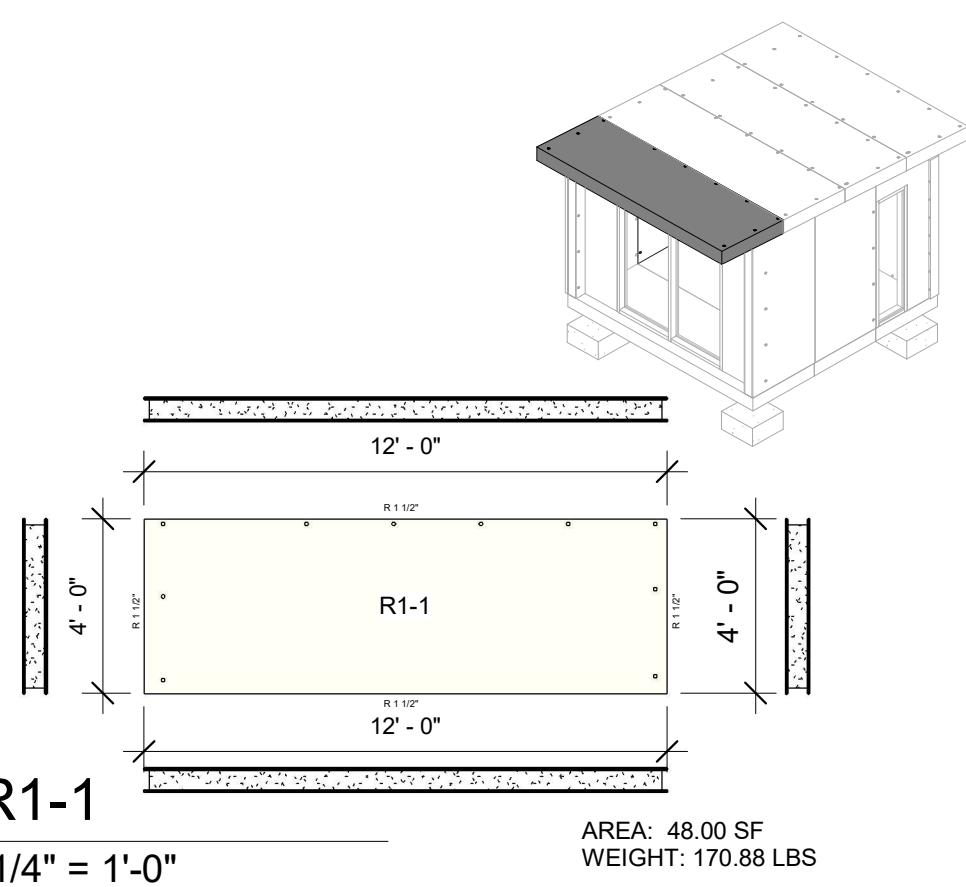


VIEW DETAILS THAT APPLY:

2 / A105
5 / A105

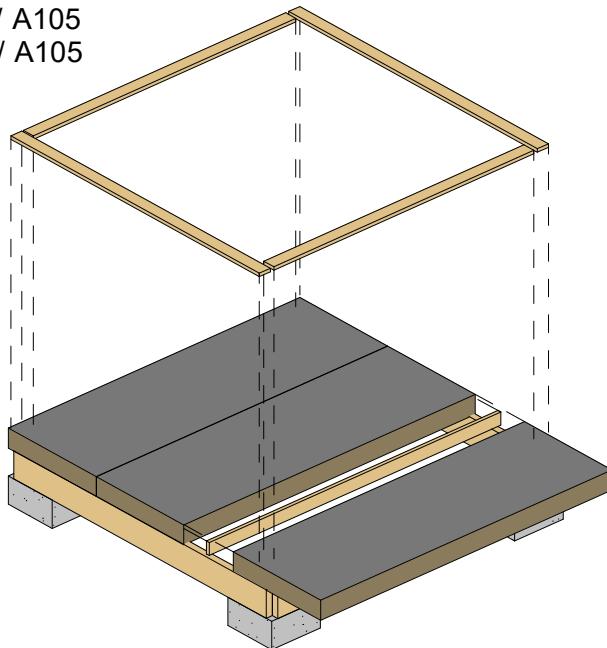


VIEW DETAILS THAT APPLY:

7 / A105
5 / A105
2 / A105

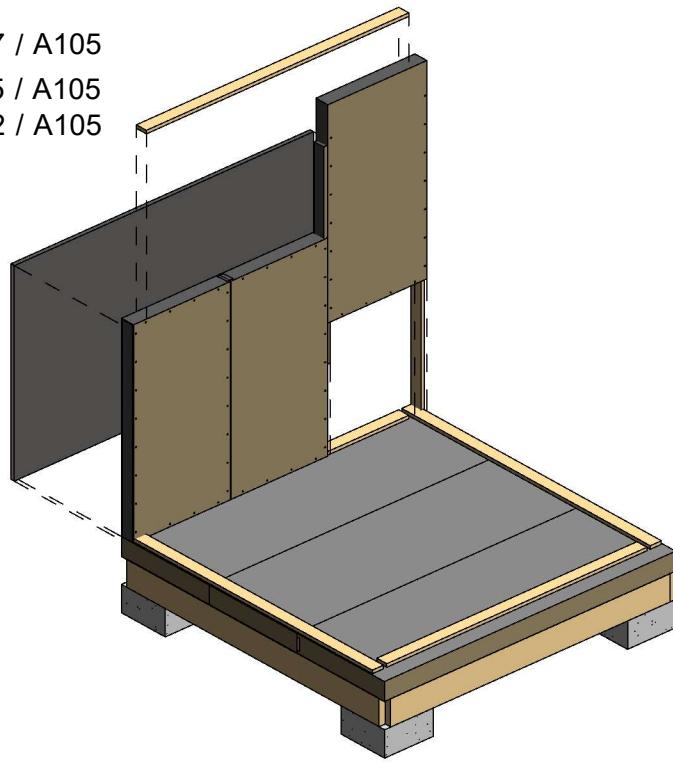


VIEW DETAILS THAT APPLY:

7 / A105
1 / A105
2 / A105
5 / A105

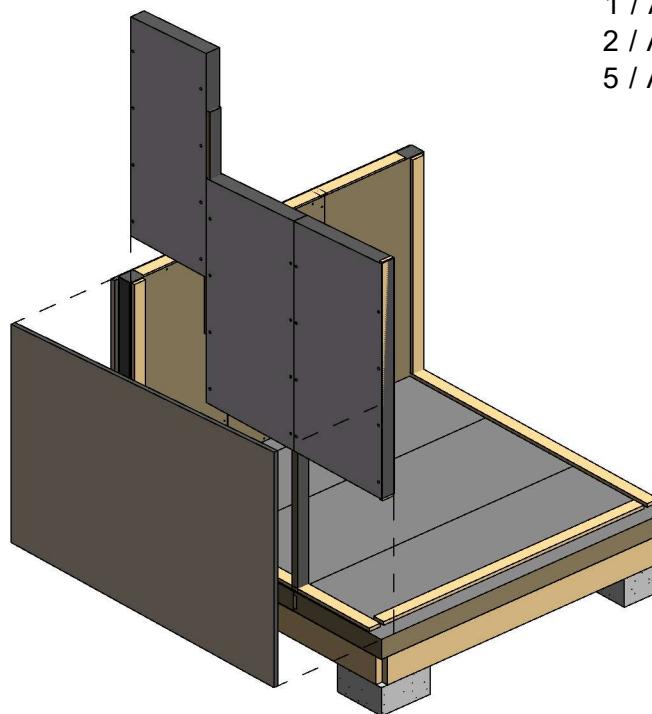


VIEW DETAILS THAT APPLY:

1 / A105
2 / A105
5 / A105
8 / A105
7 / A105

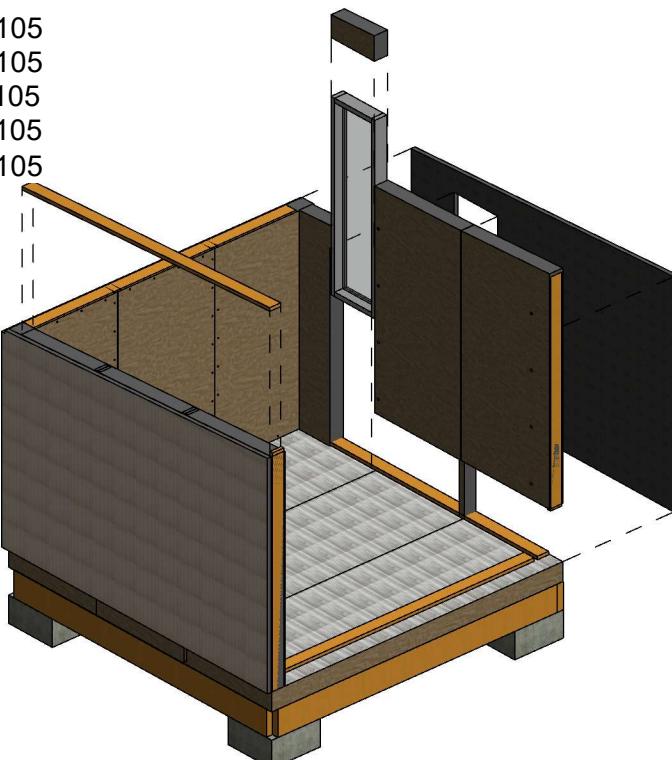


VIEW DETAILS THAT APPLY:

1 / A105
2 / A105
5 / A105
8 / A105
7 / A105

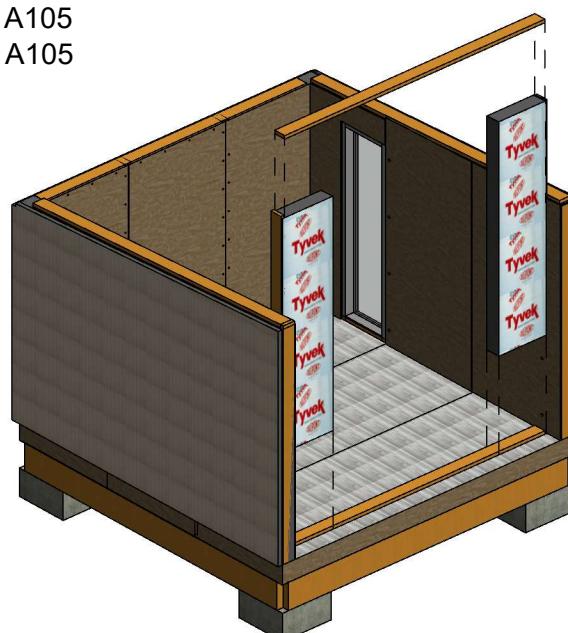

VIEW DETAILS THAT APPLY:

1 / A105
2 / A105
5 / A105
8 / A105
7 / A105

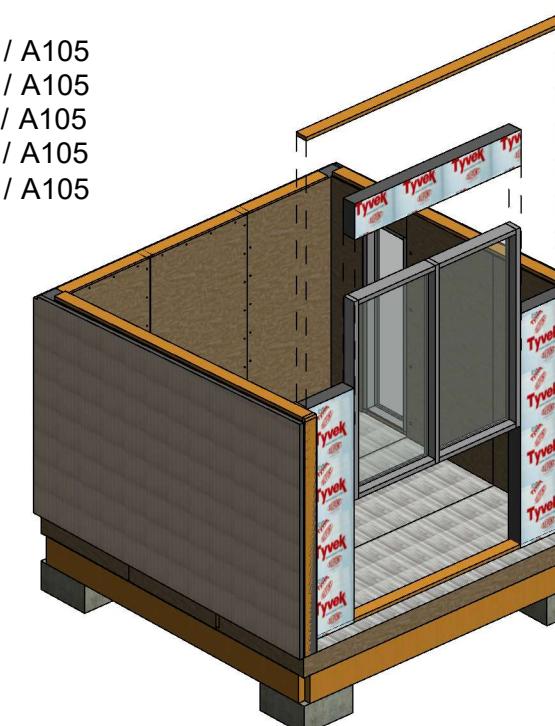

P R E F L E X
b u i l d i n g

CABIN143SF



P R E F L E X O F F I C E

No.	Description	Date

Assembly Manual

Project number Project
Number




Date Issue Date

Drawn by Author

Checked by Checker


A114

Scale

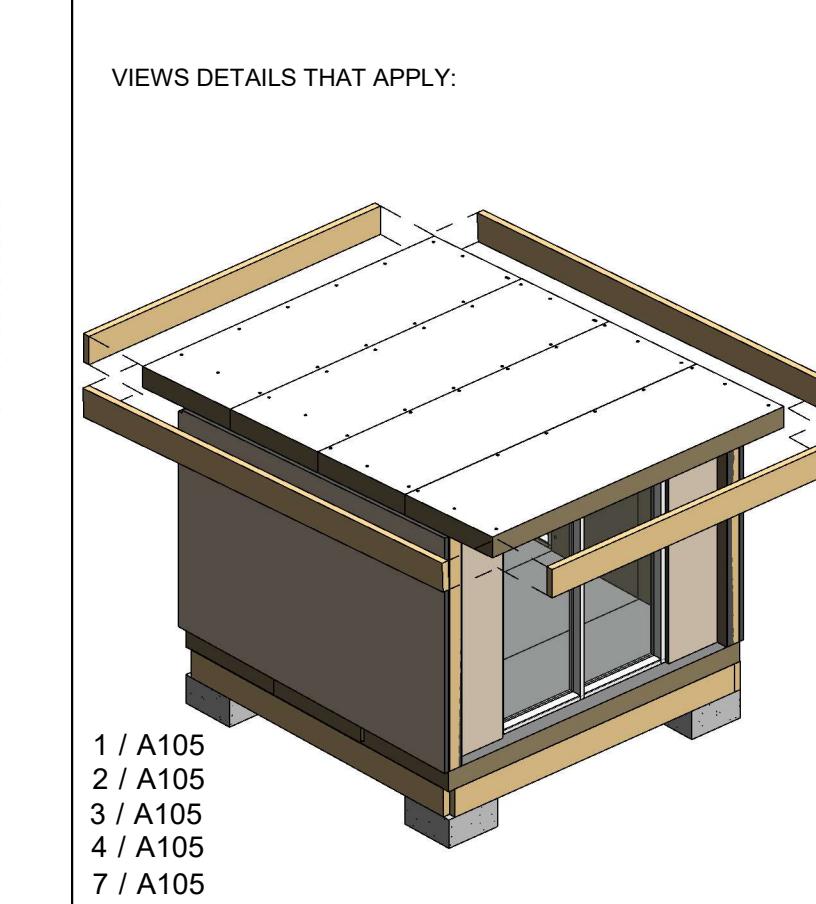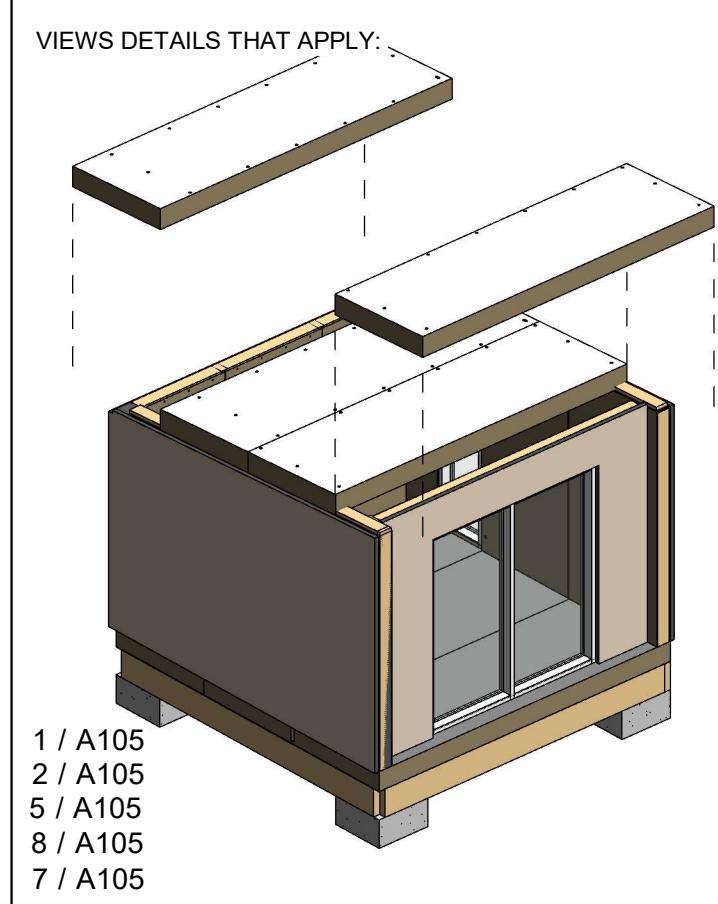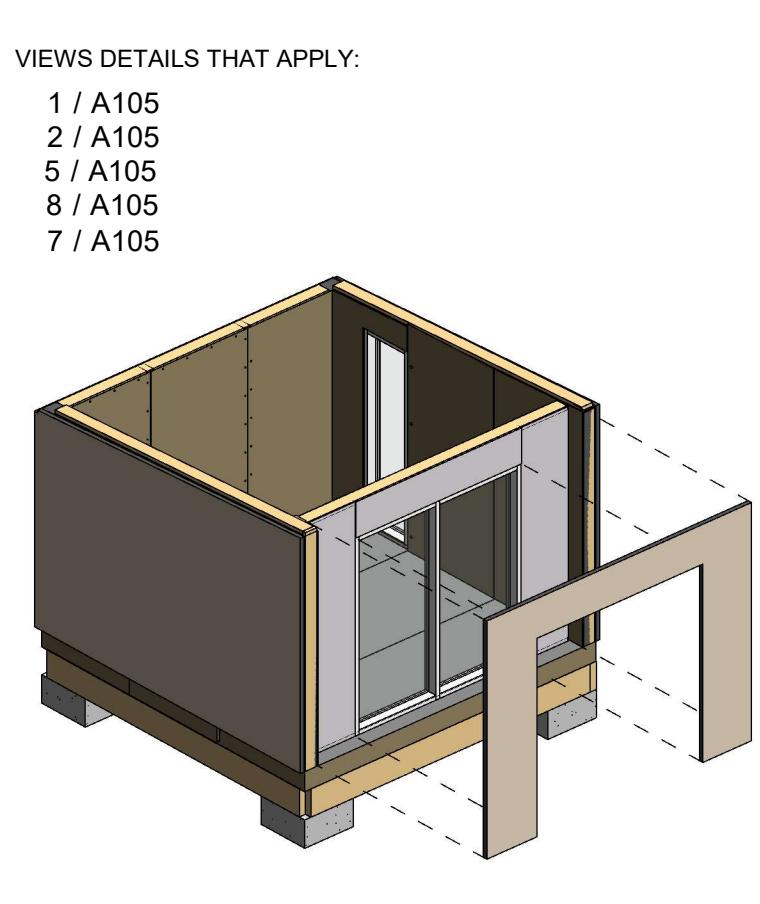


	P R E F L E X	
	b u i l d i n g	
CABIN143SF		
	P R E F L E X O F F I C E	
No.	Description	Date
Assembly Manual		
Project number	Project Number	
Date	Issue Date	
Drawn by	Author	
Checked by	Checker	
A115		
Scale		


14/06/2021 04:24:05 p. m.

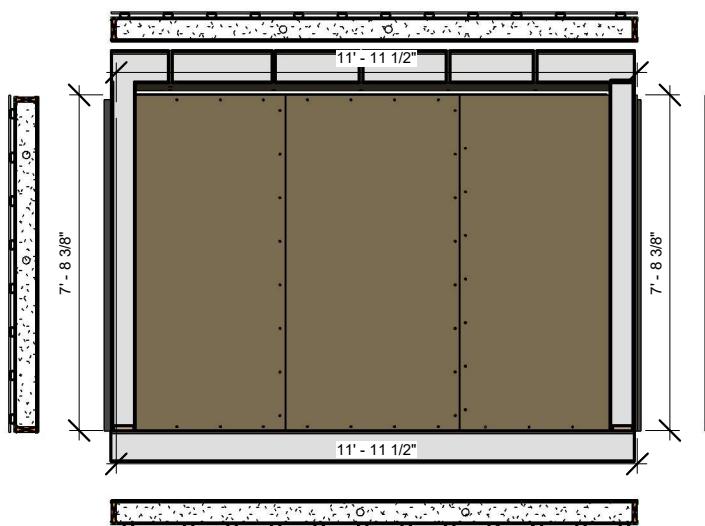


1 MW_1
1/4" = 1'-0"

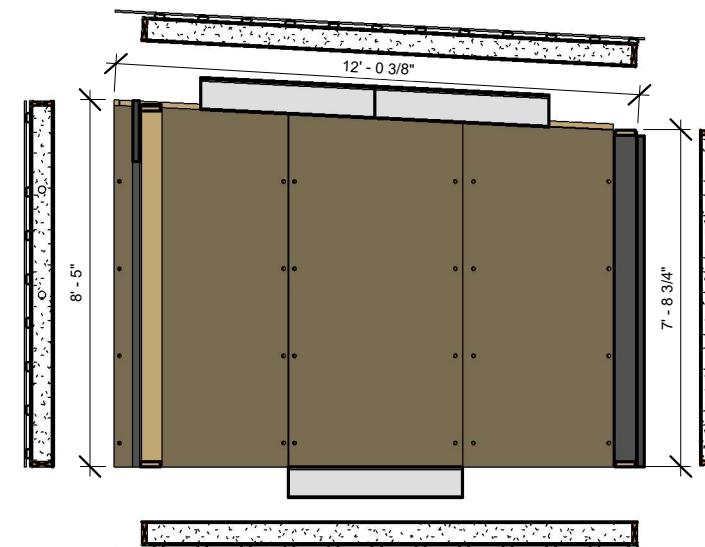


2 MW_2
1/4" = 1'-0"

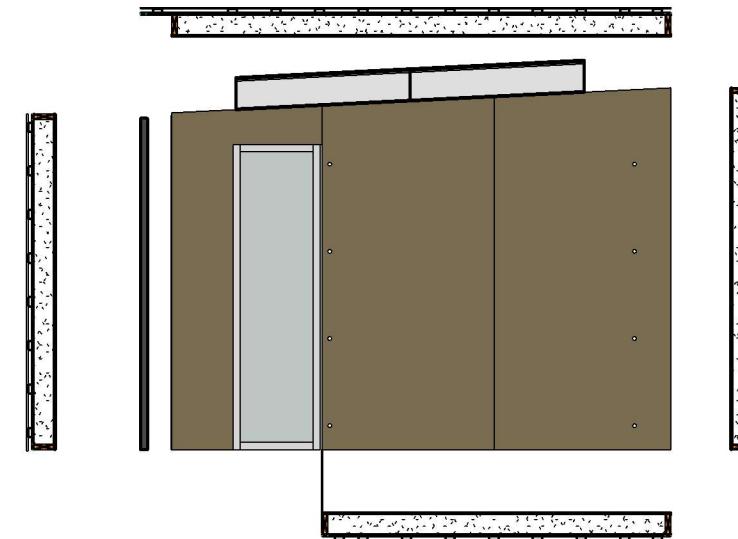

3 MW_3
1/4" = 1'-0"

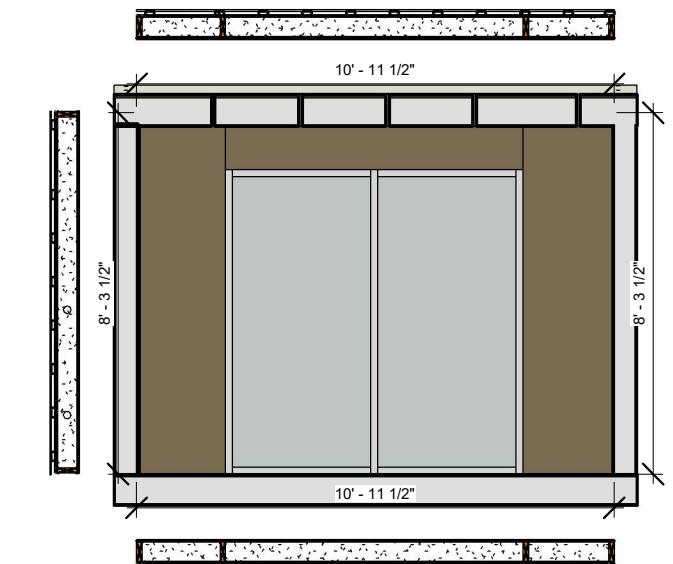

4 MW_4
1/4" = 1'-0"

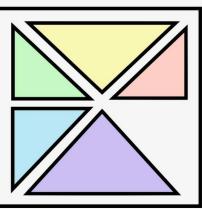

P R E F L E X
b u i l d i n g

CABIN143SF



P R E F L E X O F F I C E

No.	Description	Date

Interior Views

Project number	Project Number
Date	Issue Date
Drawn by	Author
Checked by	Checker

A116

Scale 1/4" = 1'-0"